

UTILITAS BANGUNAN GEDUNG K

KELOMPOK 4

ALVIN LORENZA

ANNISA FAUZIA

ASTARI DWINA B.

DINI PUTI A.

DRASTHYA A. N.


ELIZA STEPHANIE

QATRUN NADA

RAHMADANI MARTA


A. TATA UDARA

DENAH RENCANA TATA UDARA LANTAI 1

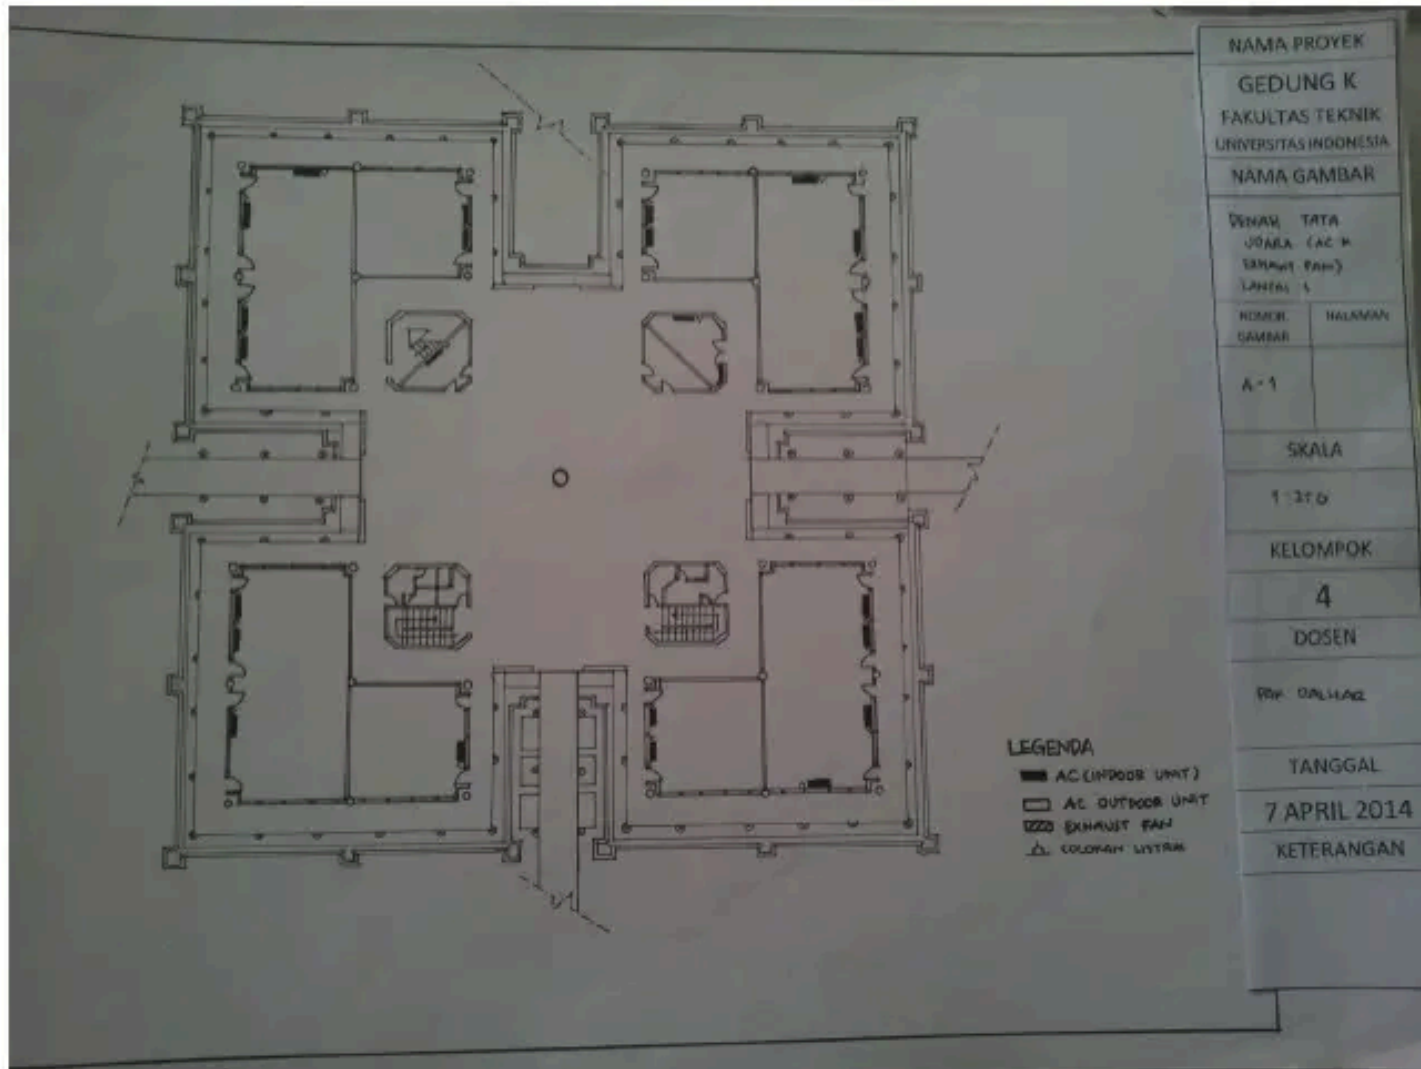


DENAH RENCANA TATA UDARA

LANTAI 2

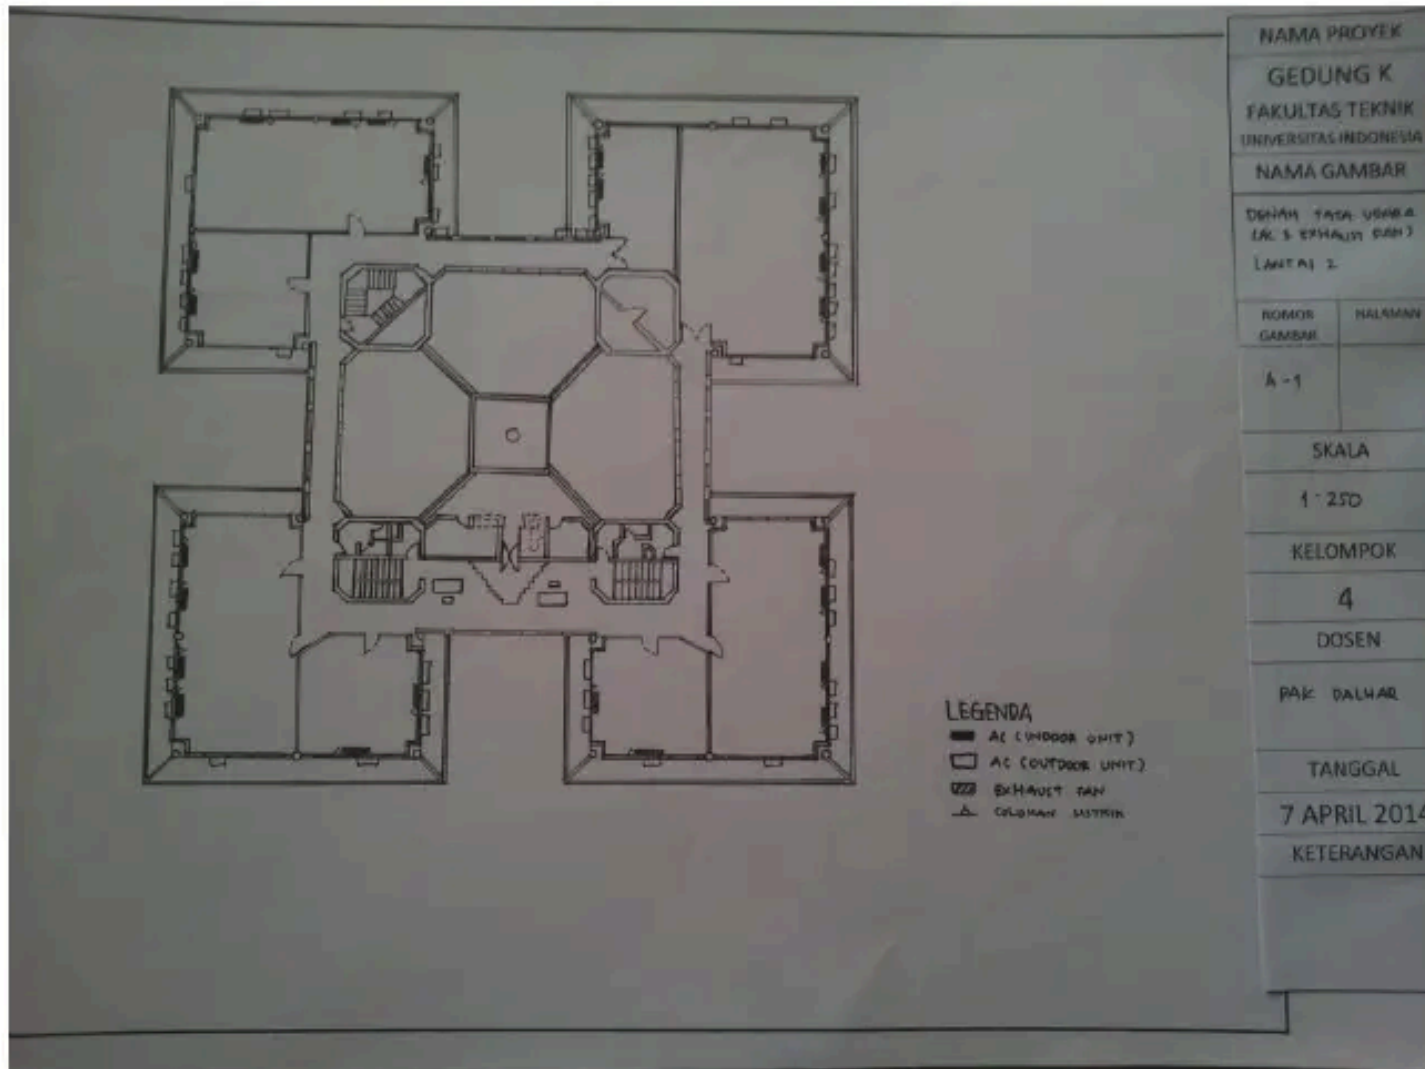


NAMA PROYEK	
GEDUNG K	
FAKULTAS TEKNIK	
UNIVERSITAS INDONESIA	
NAMA GAMBAR	
DENAH TATA UDARA (AC & EXHAUST FAN)	
LANTAI 2	
NOMOR GAMBAR	NALAMAN
A-1	
SKALA	
1 : 250	
KELOMPOK	
4	
DOSEN	
PAK DALHAR	
TANGGAL	
7 APRIL 2014	
KETERANGAN	


DENAH RENCANA TATA UDARA LANTAI 3

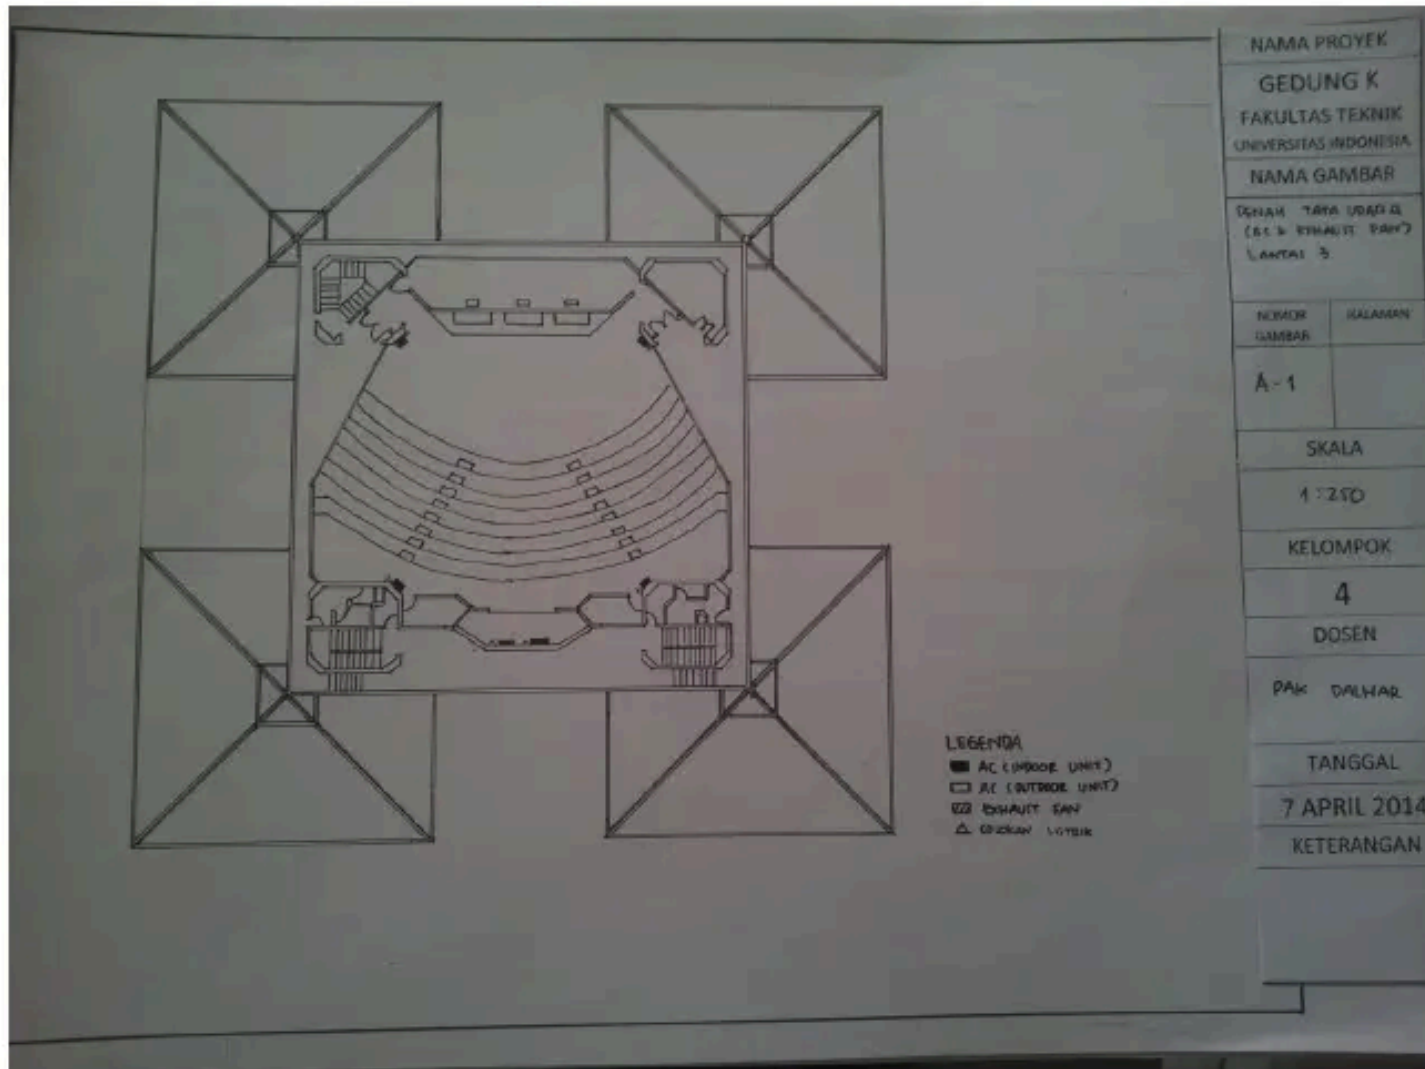


DENAH RENCANA TATA UDARA LANTAI 4

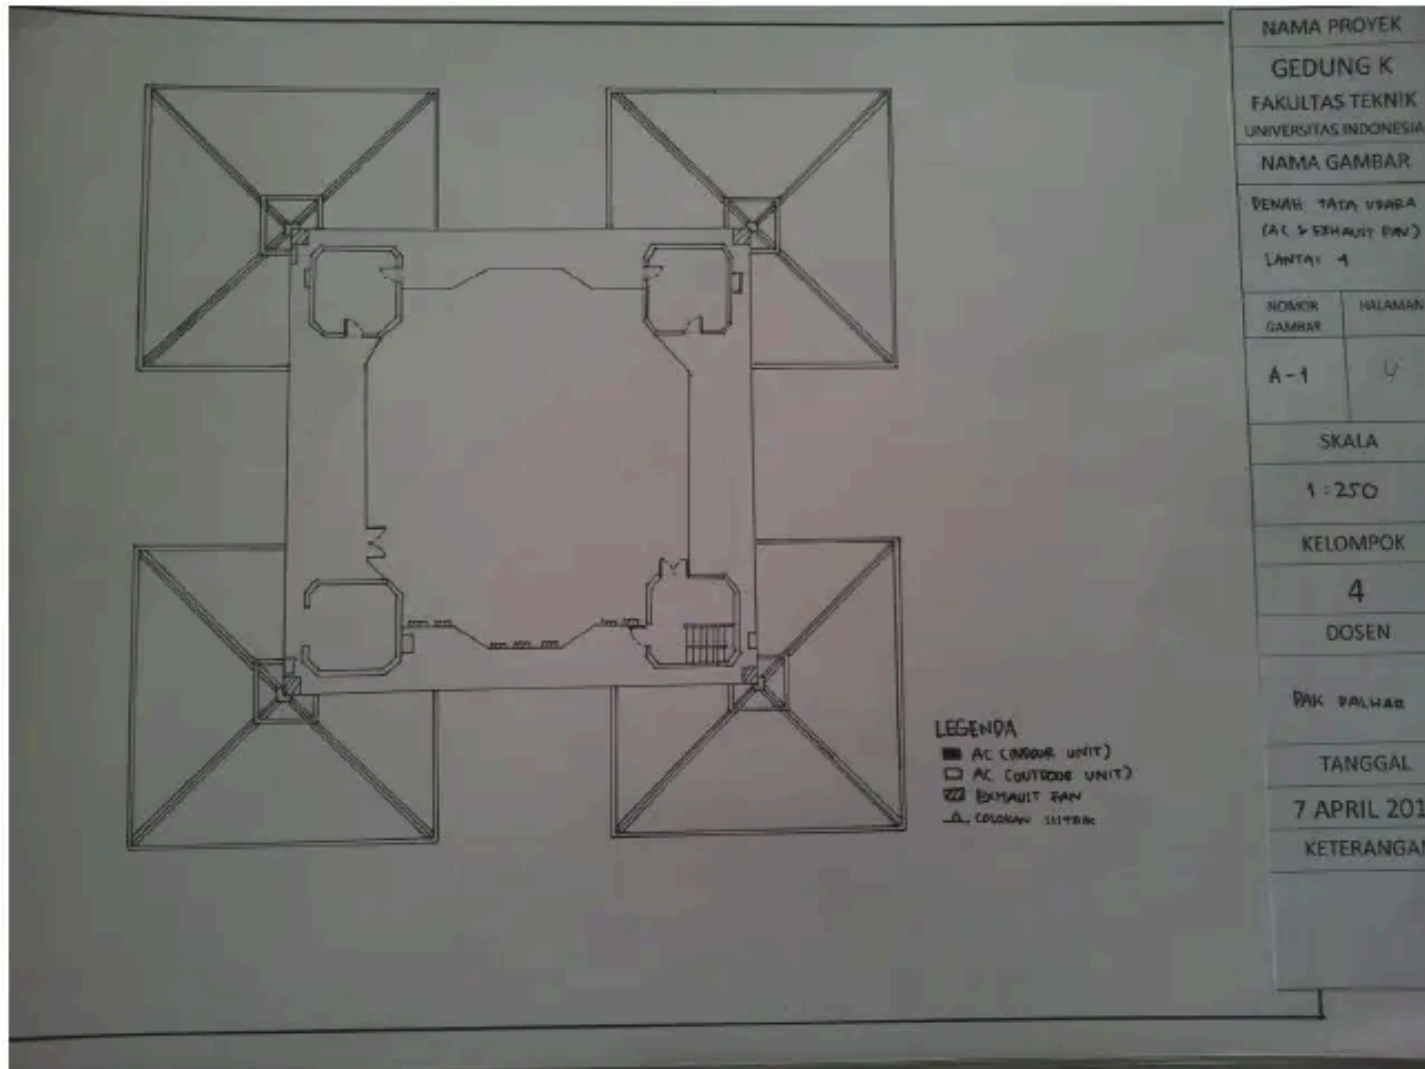

DETAIL INSTALASI TATA UDARA (EXHAUST FAN)

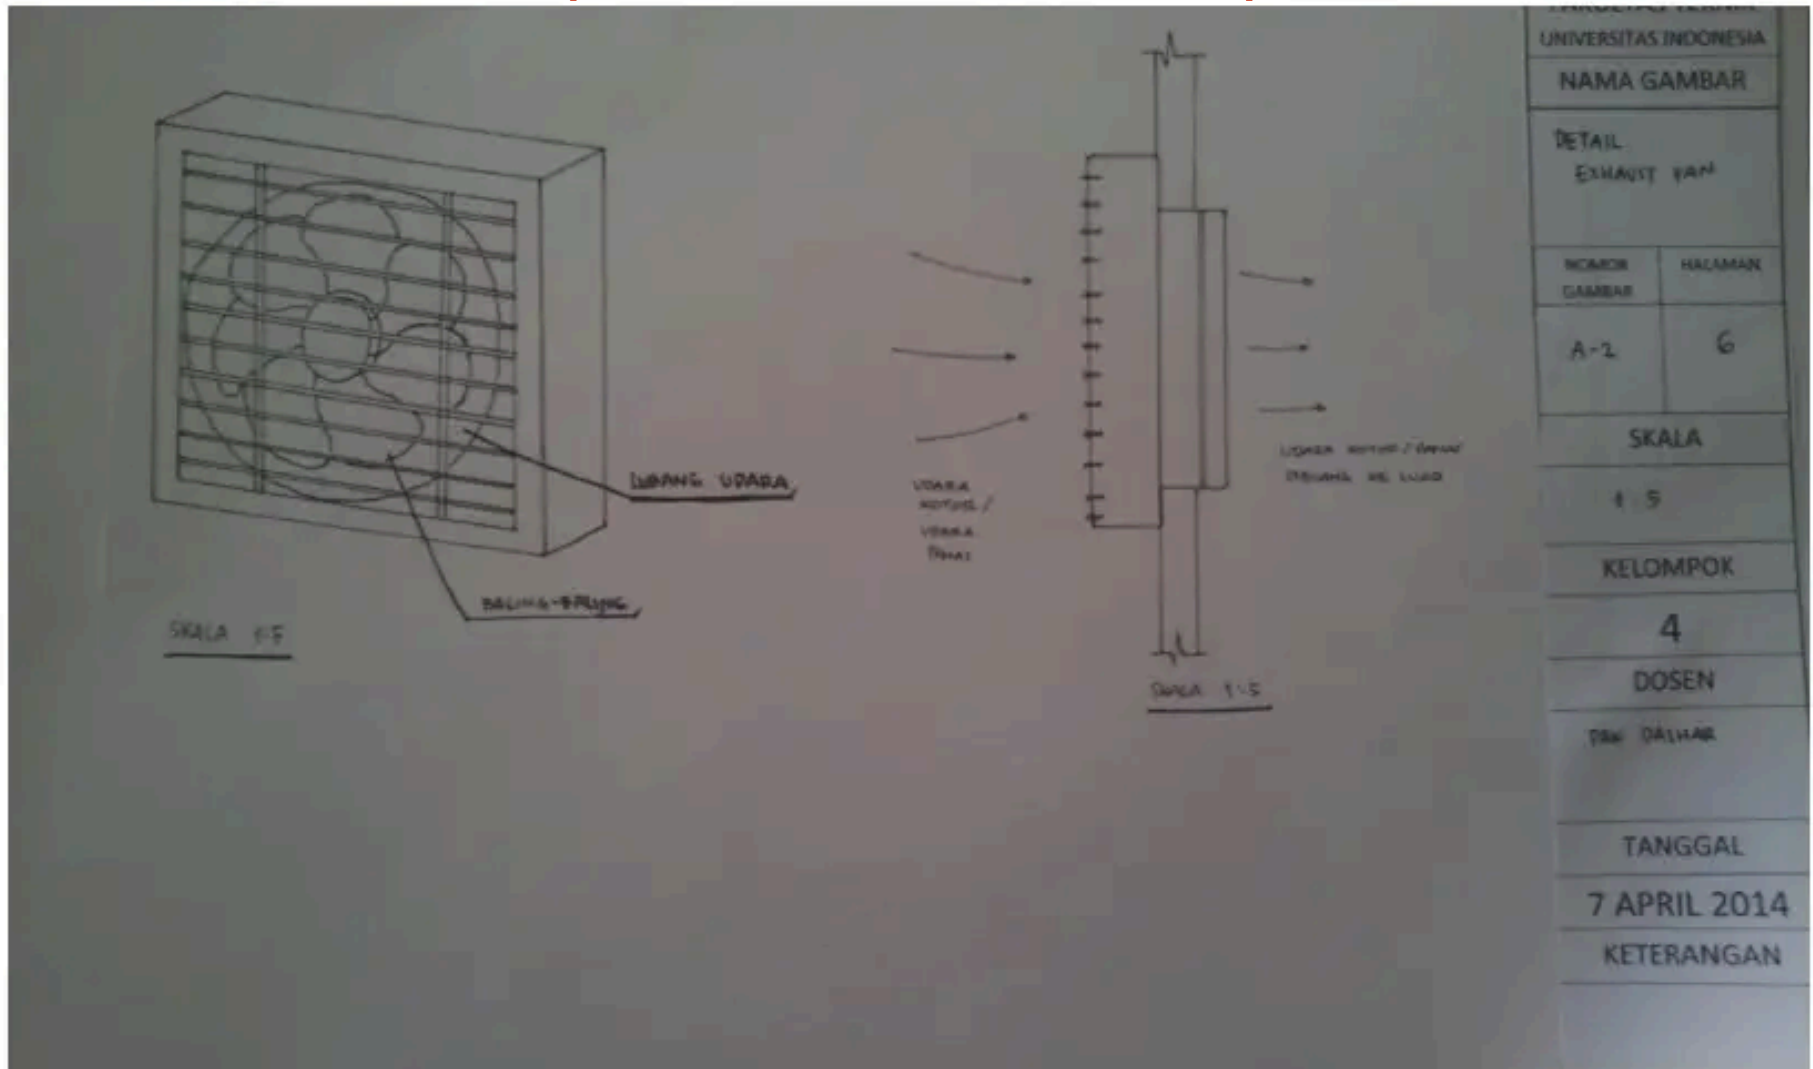

DETAIL INSTALASI TATA UDARA (AC)

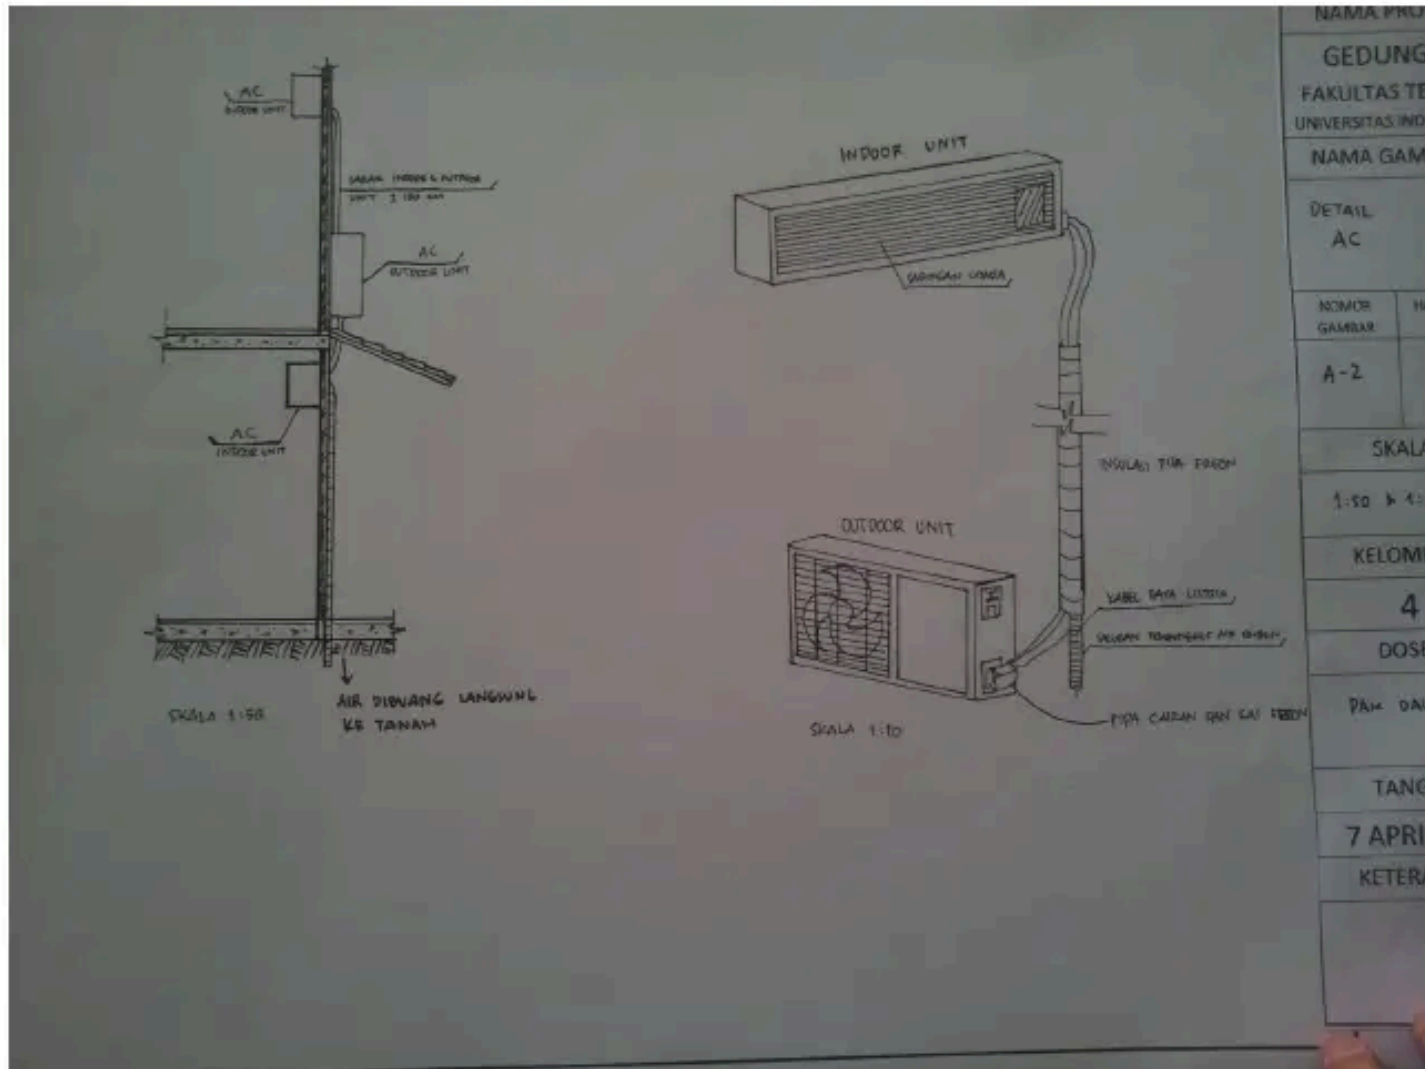

NAMA PROJEK

GEDUNG

FAKULTAS TEKNIK
UNIVERSITAS INDONESIA

NAMA GAMBAR

DETAIL
AC

NOMOR
GAMBAR

A-2

SKALA

1:50 & 1:10

KELOMPOK

4

DOSEN

PAK DANI

TANGGAL


7 APRIL

KETERANGAN


PLUMBING

AIR BERSIH


DIAGRAM SKEMATIK PEMIPAAN AIR BERSIH SATU GARIS

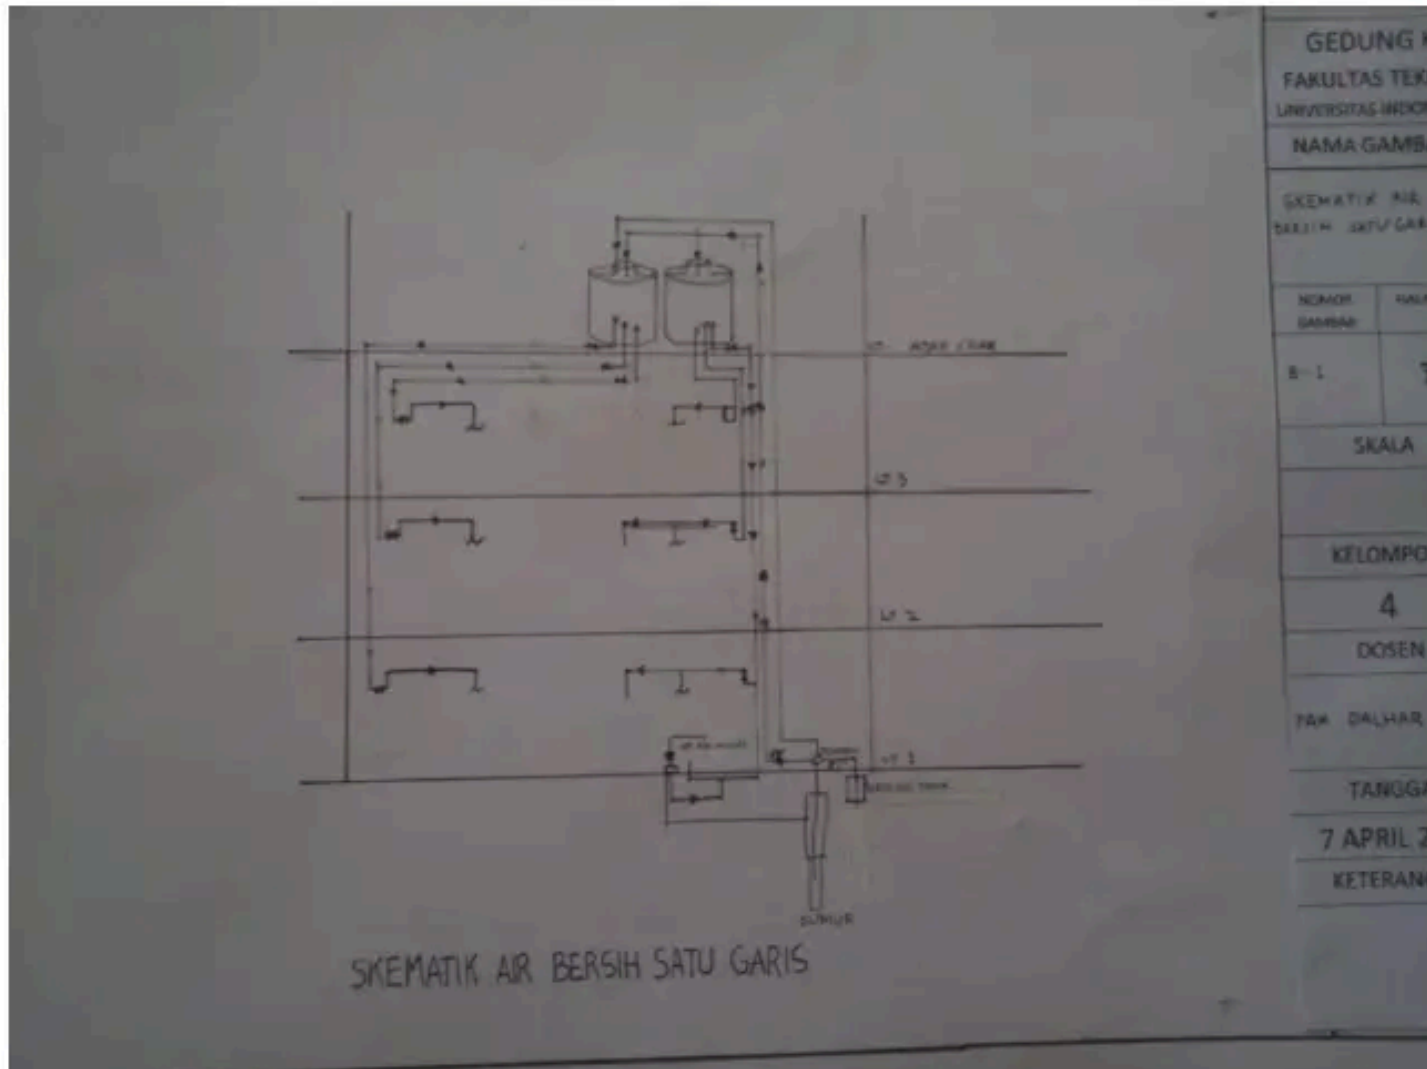


ISOMETRIK PEMIPAAN AIR BERSIH

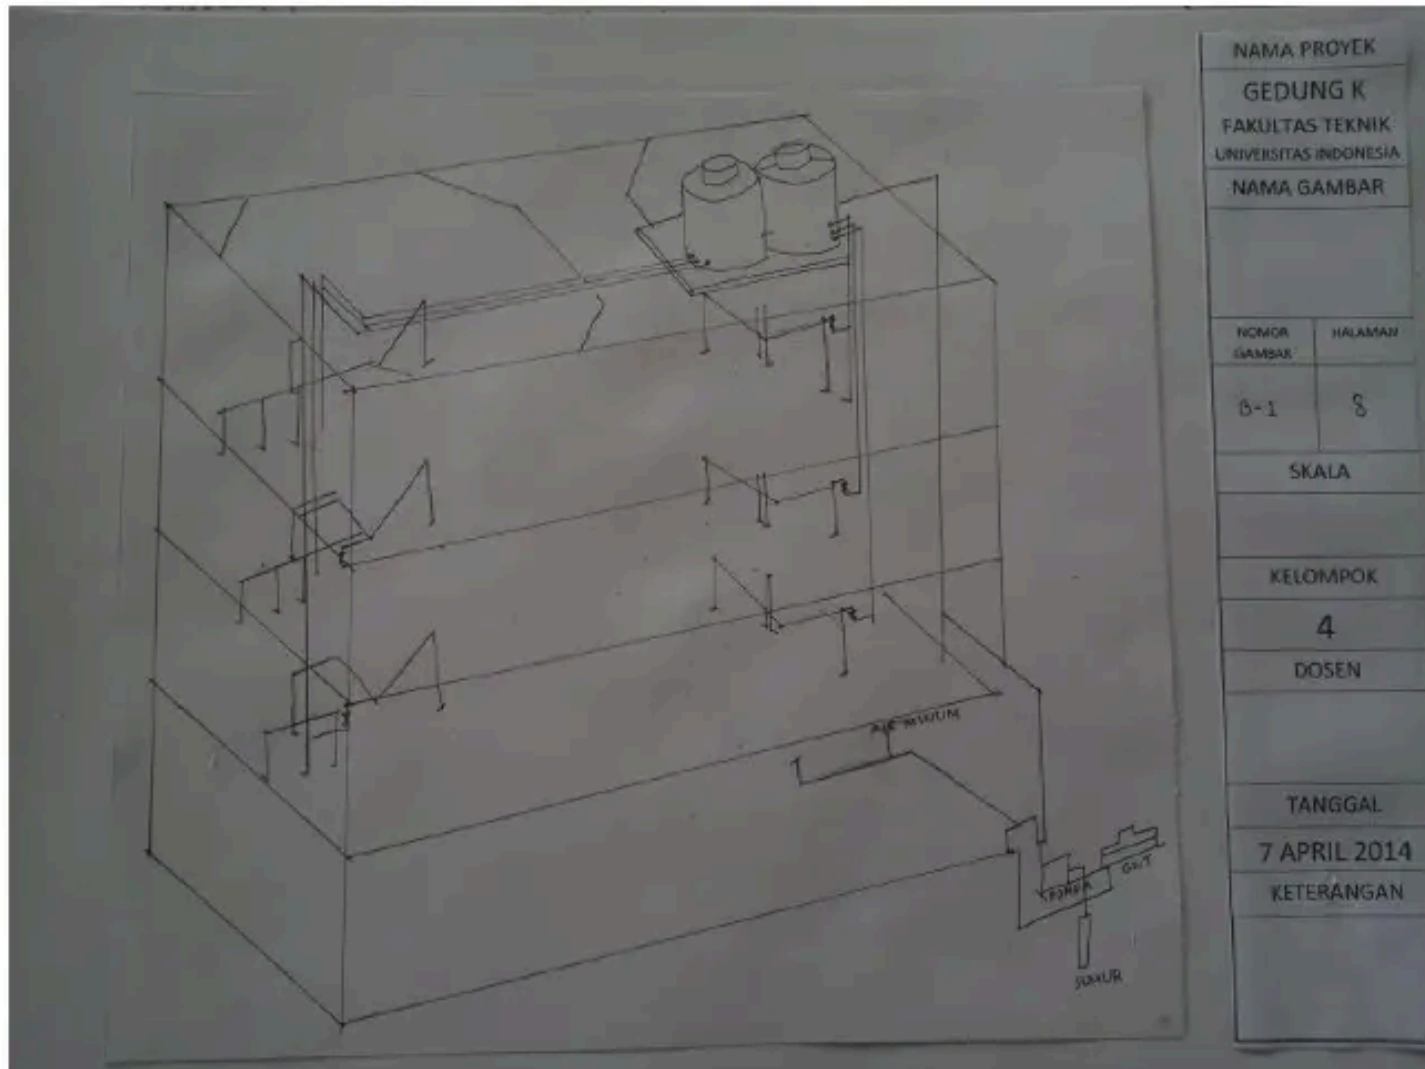


DENAH PEMIPAAN AIR BERSIH LANTAI DASAR

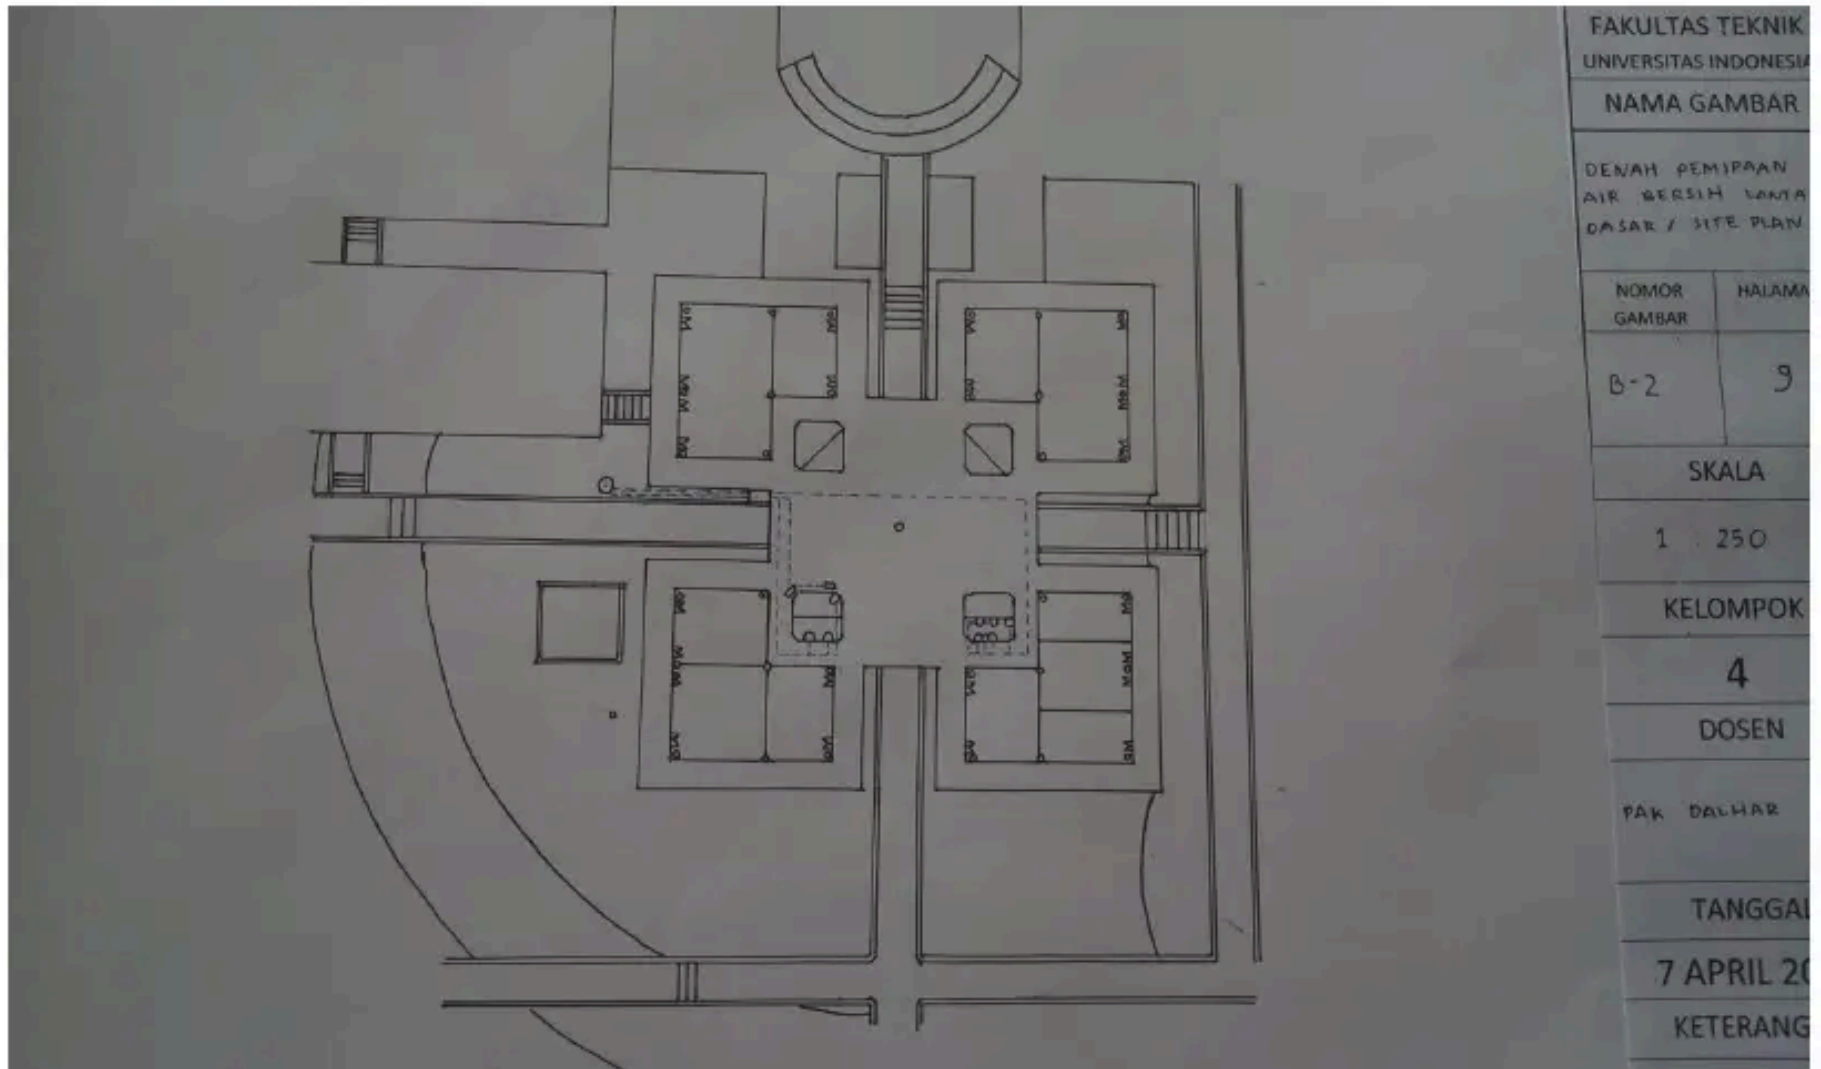


DETAIL DENAH PEMIPAAN AIR BERSIH LANTAI ROOF TANK

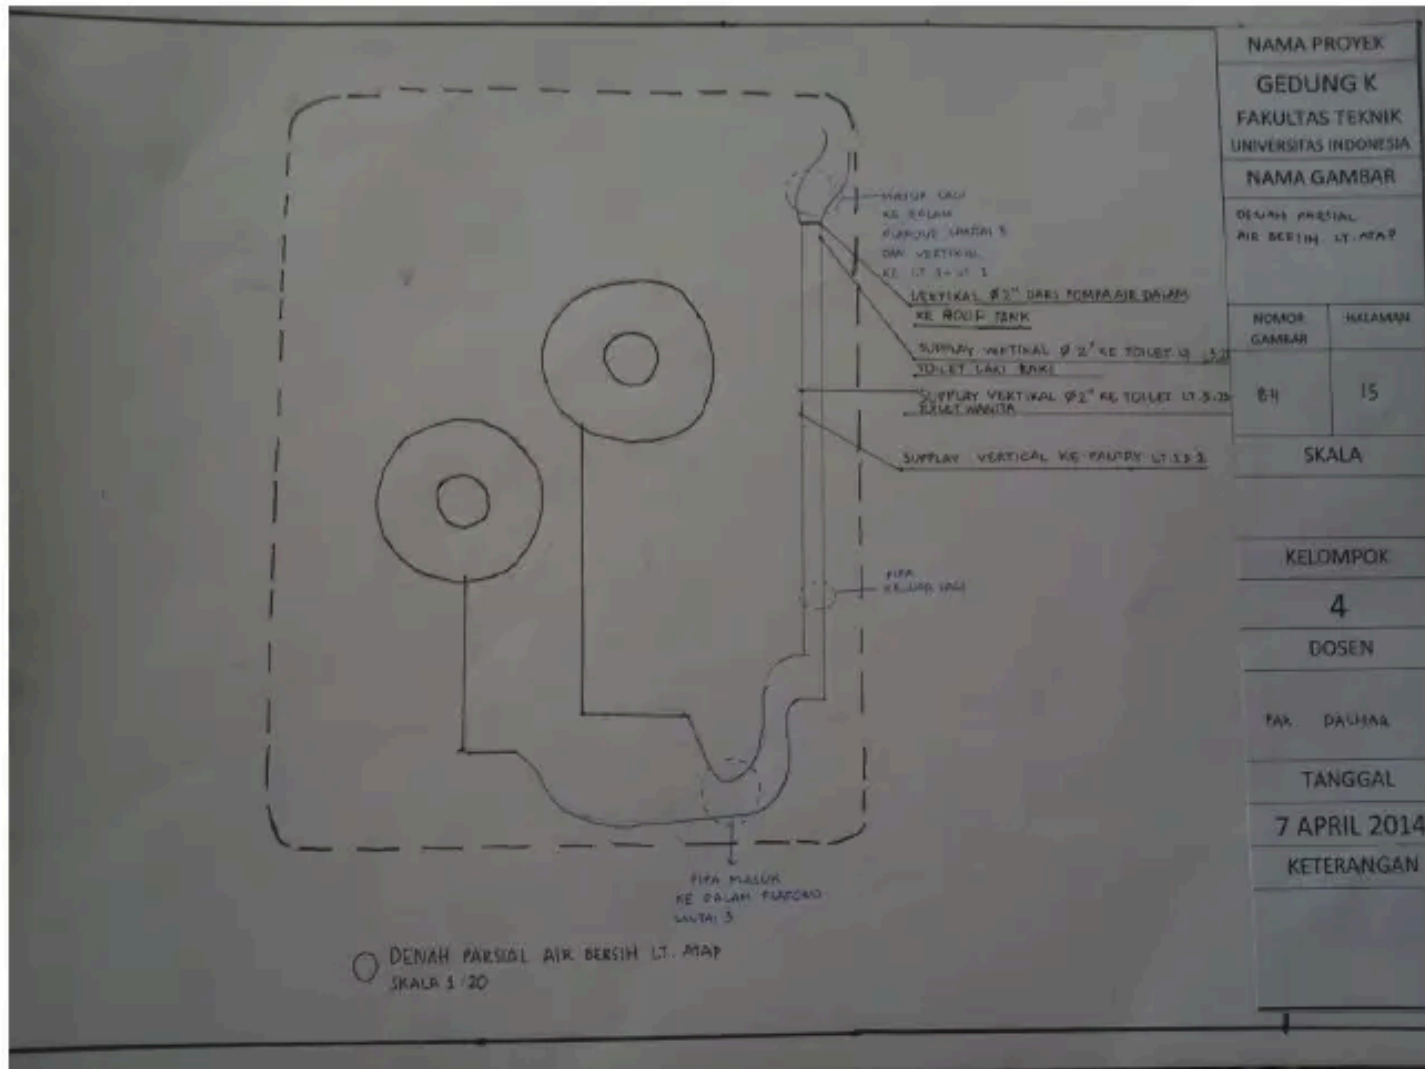


DETAIL DENAH PEMIPAAN AIR BERSIH LANTAI 4

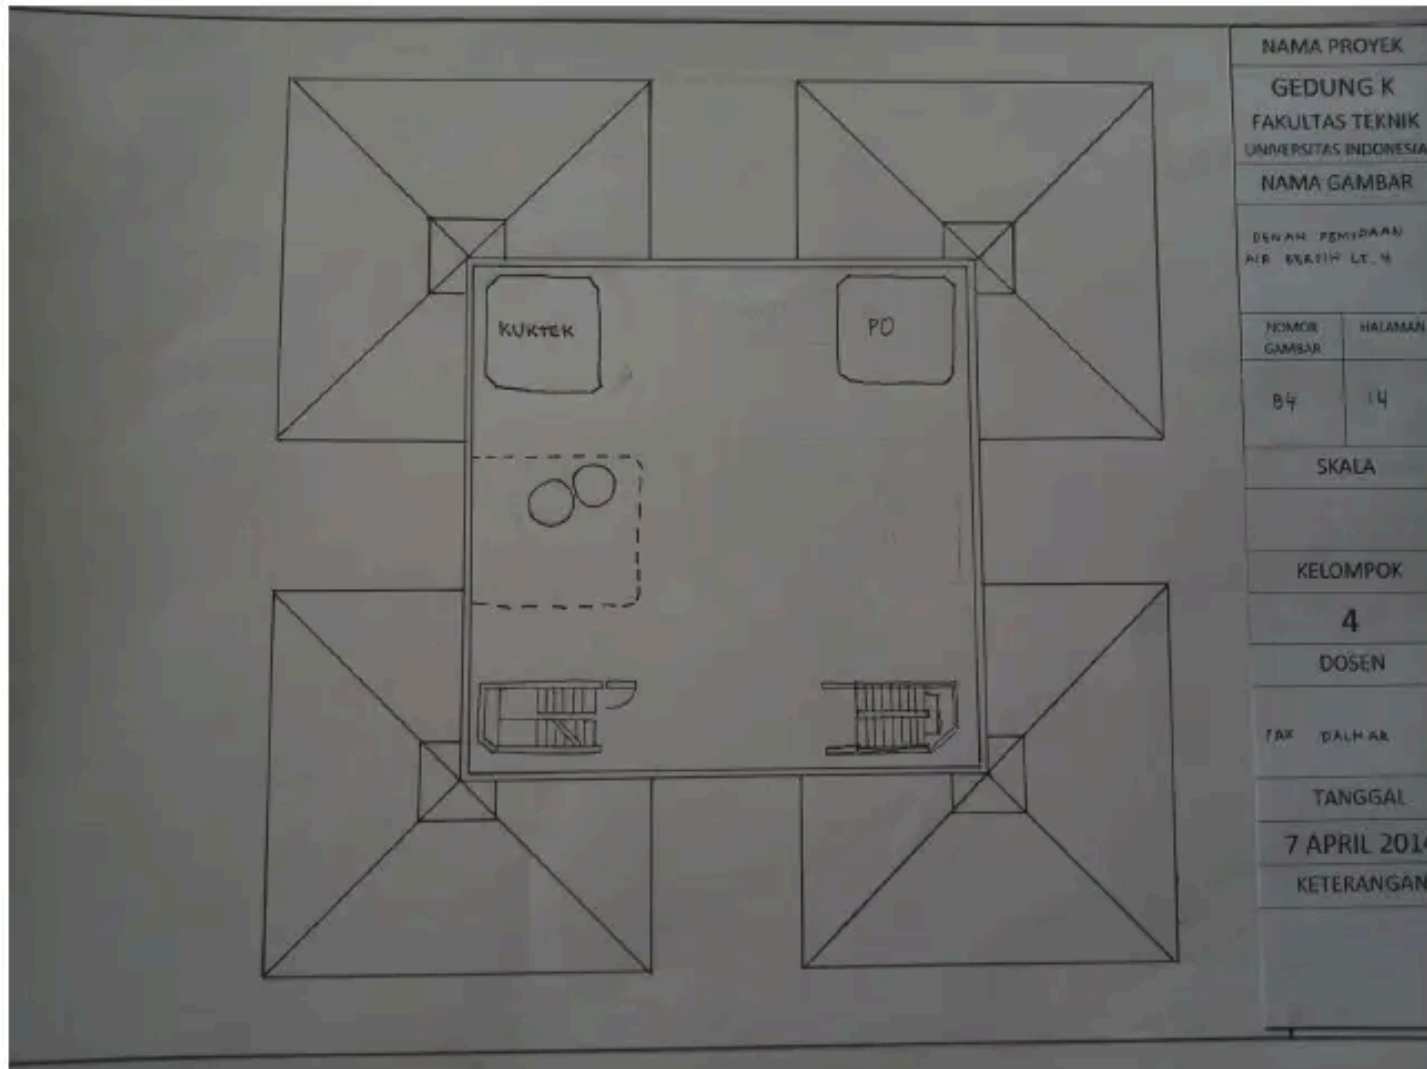


DETAIL DENAH PEMIPAAN AIR BERSIH LANTAI 2-3 (PANTRY)

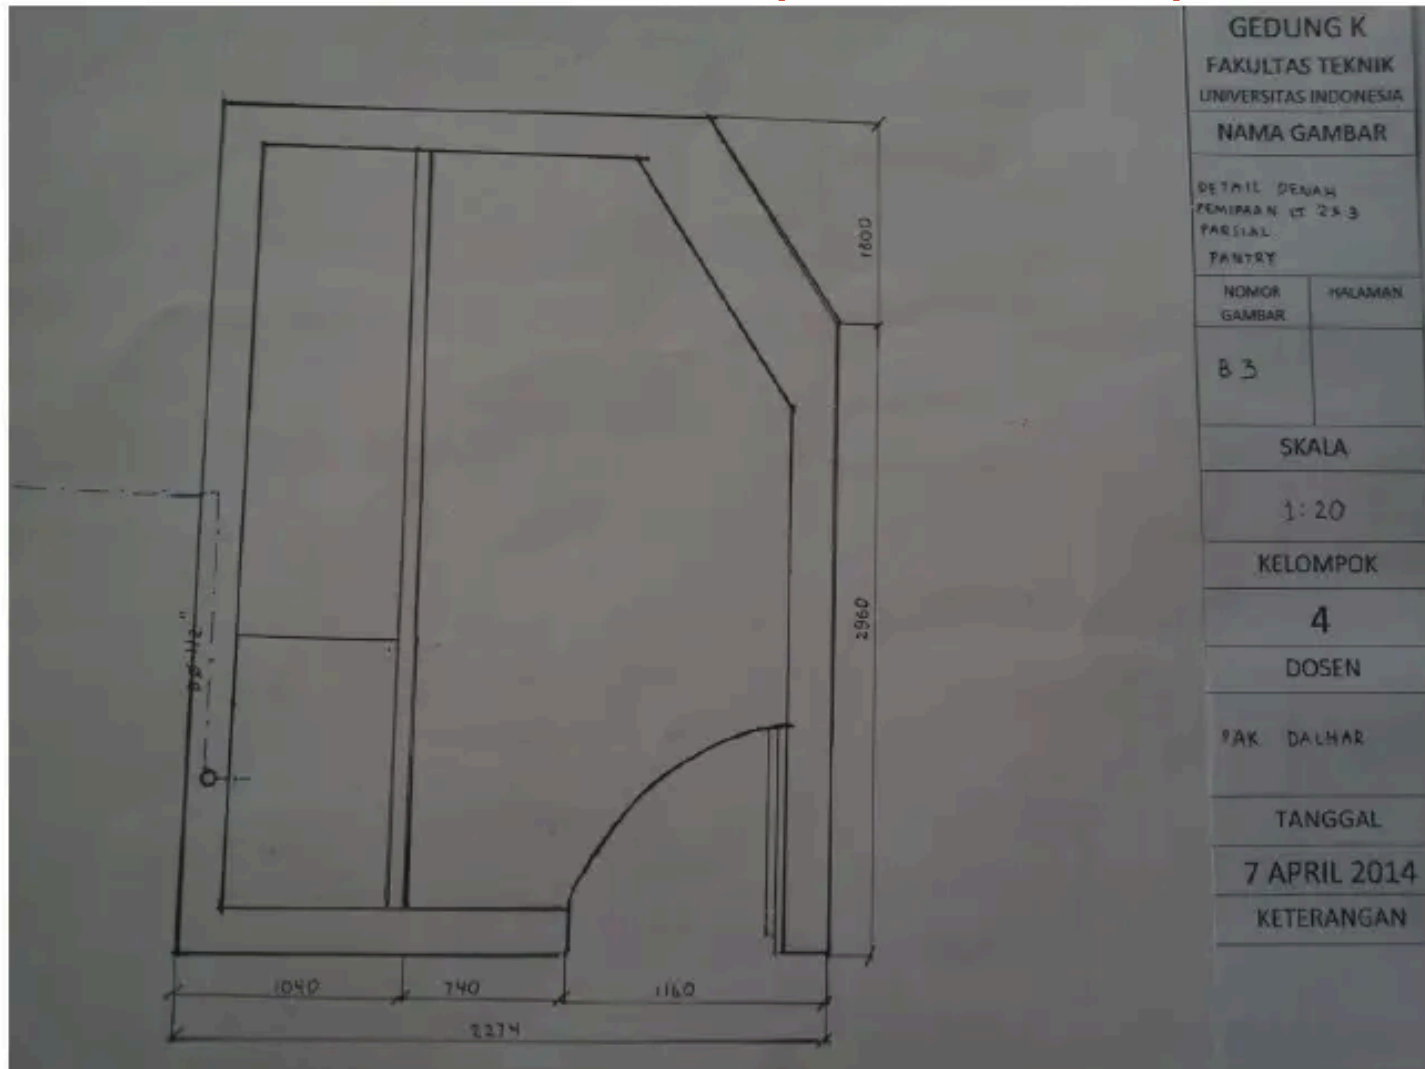


DETAIL DENAH PEMIPAAN AIR BERSIH LANTAI 1-4 (TOILET LAKI-LAKI)

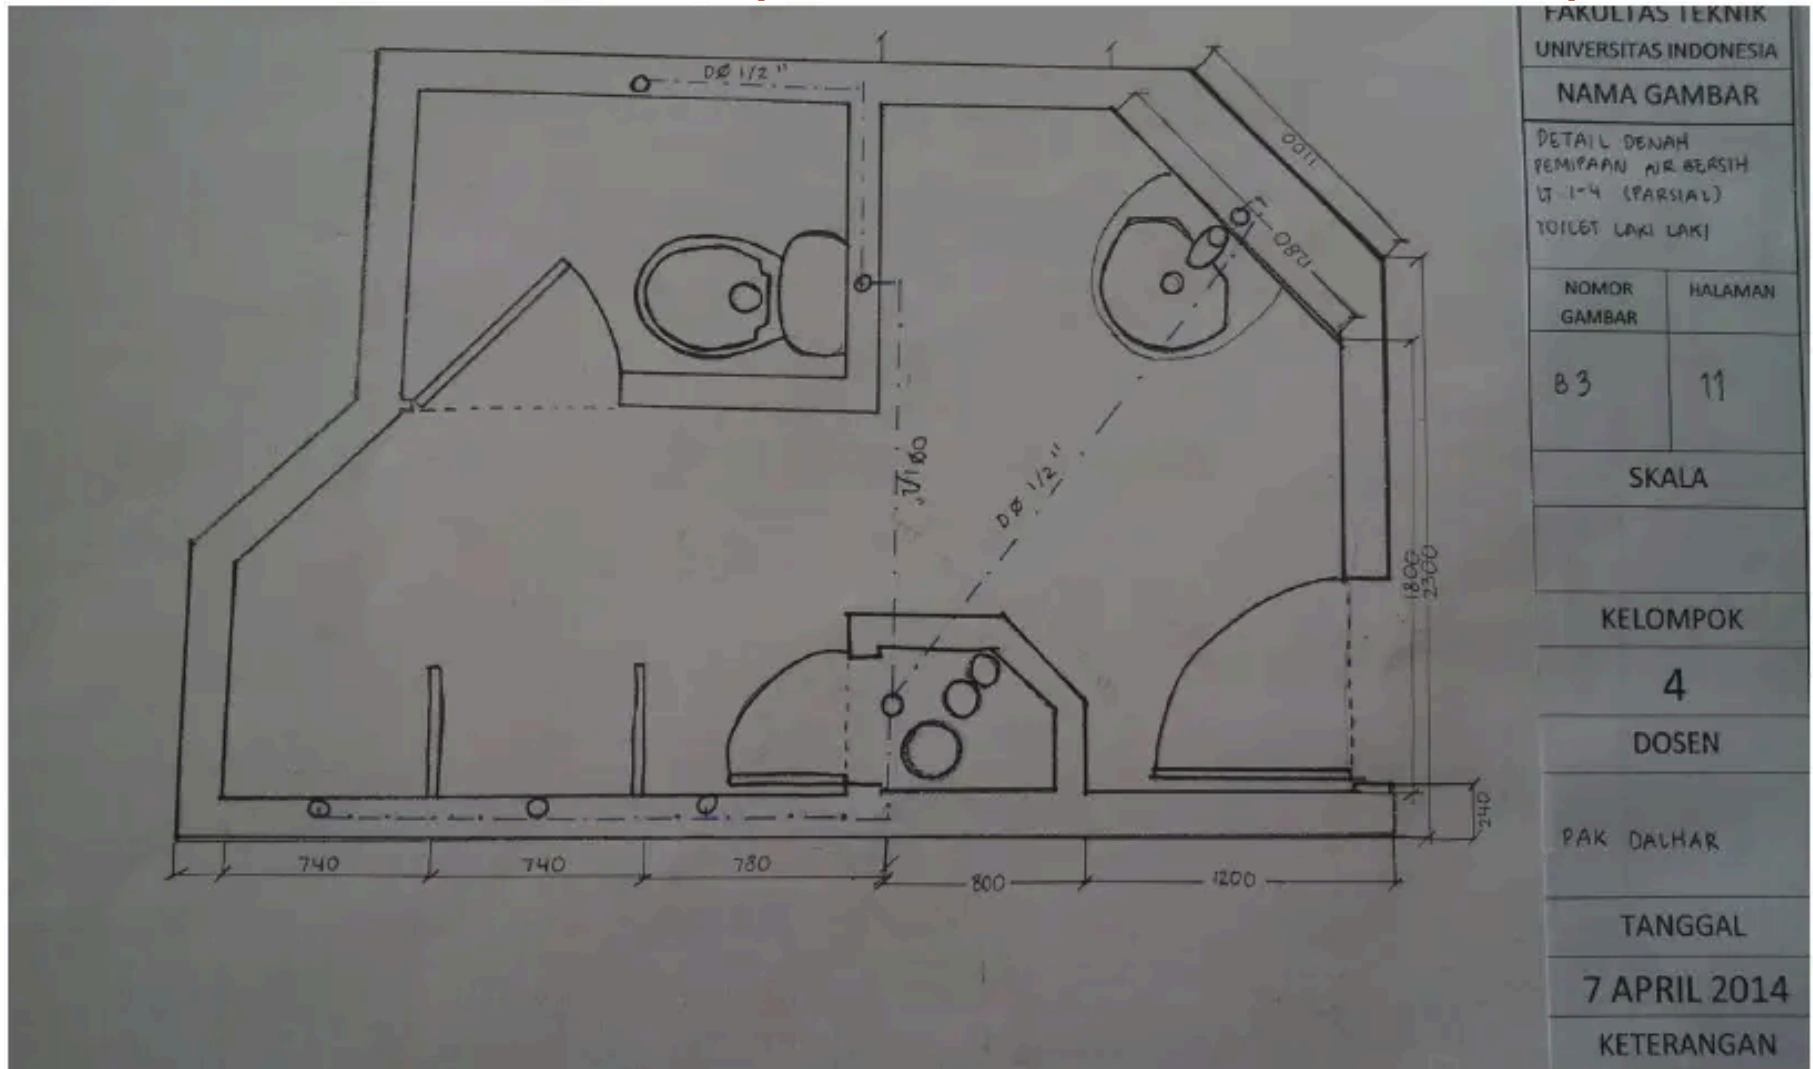

DETAIL DENAH PEMIPAAN AIR BERSIH LANTAI 1-4 (TOILET PEREMPUAN)

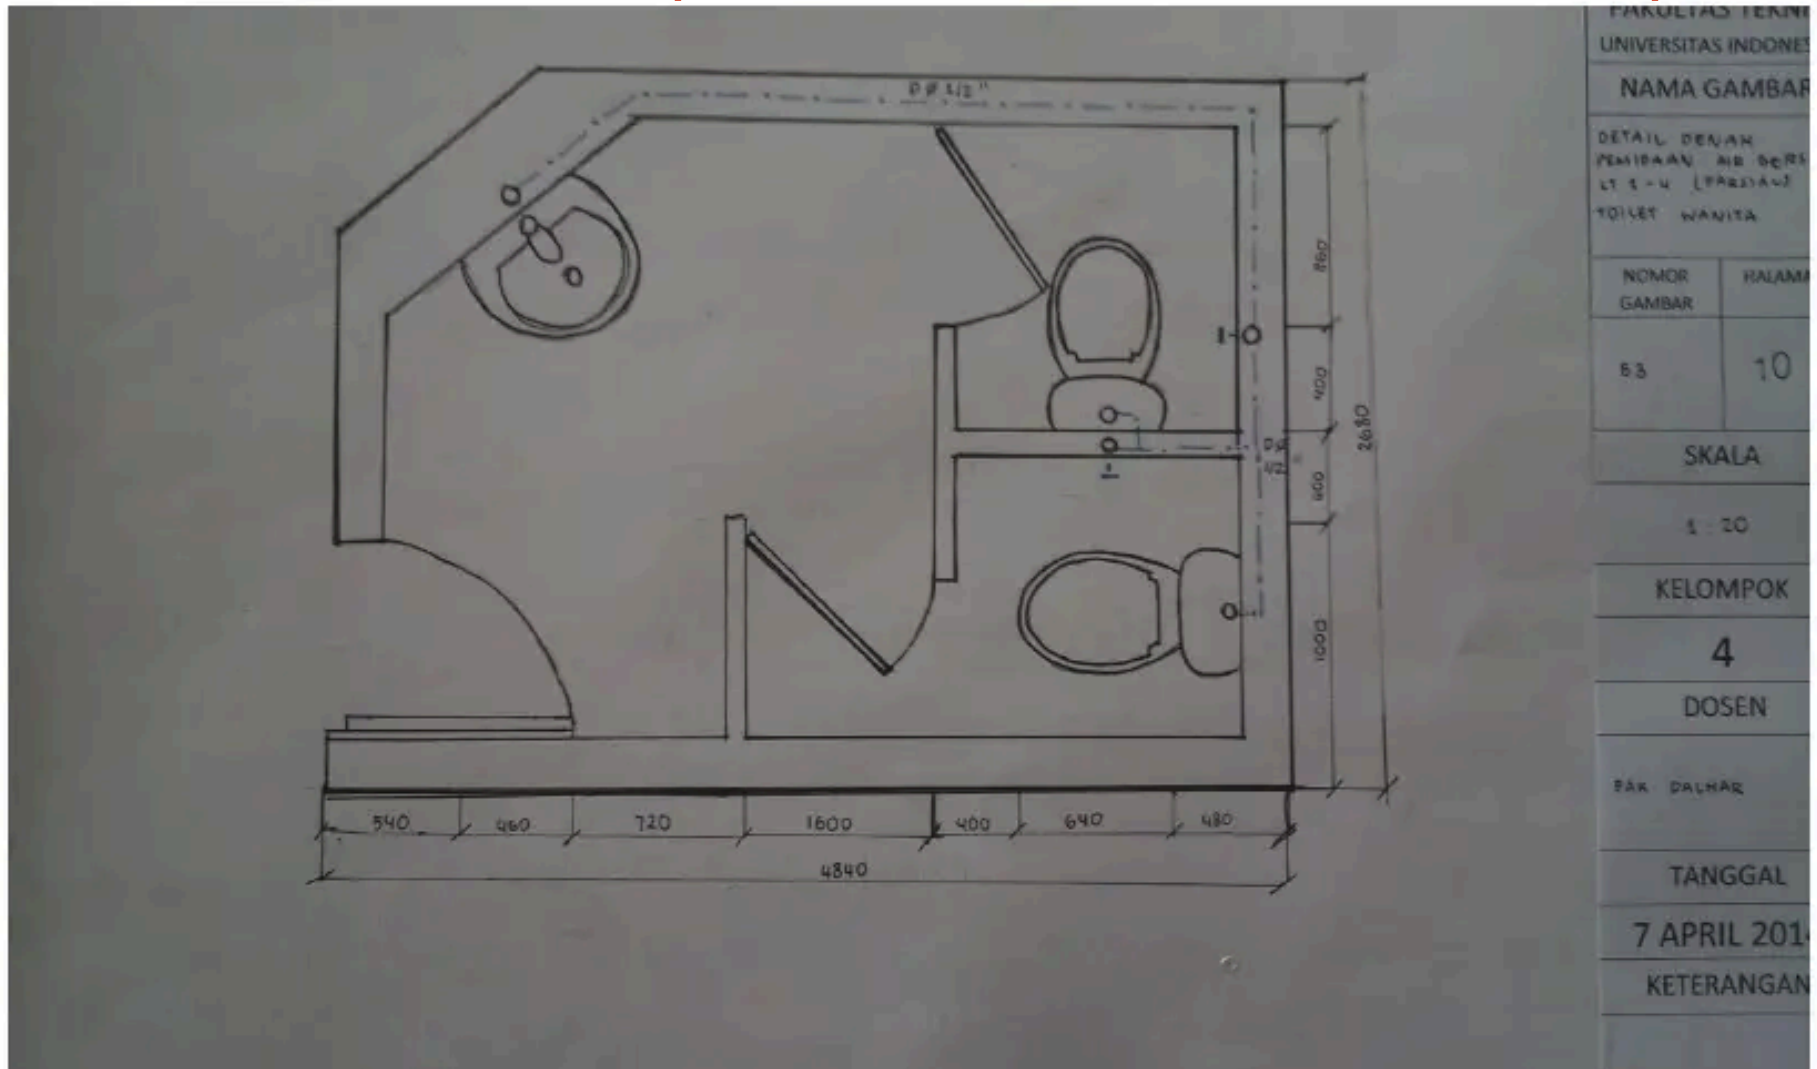


DETAIL GROUND TANK DAN INSTALASI POMPA SUMUR

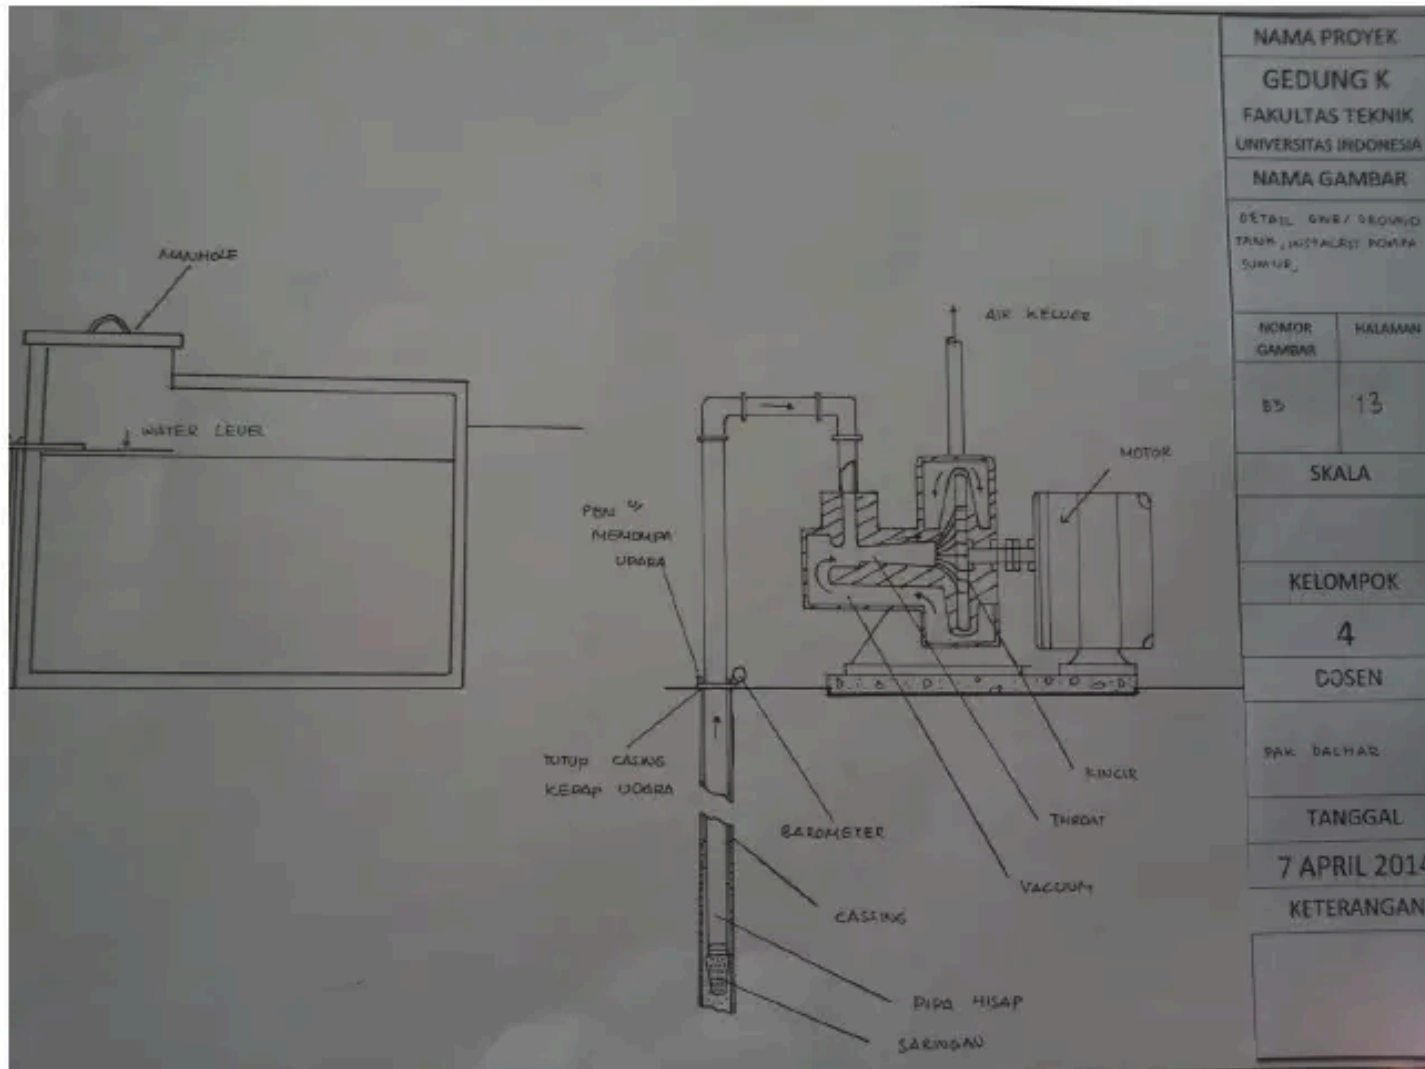


PLUMBING

AIR BEKAS DAN KOTOR


DIAGRAM SKEMATIK PEMIPAAN AIR BEKAS SATU GARIS

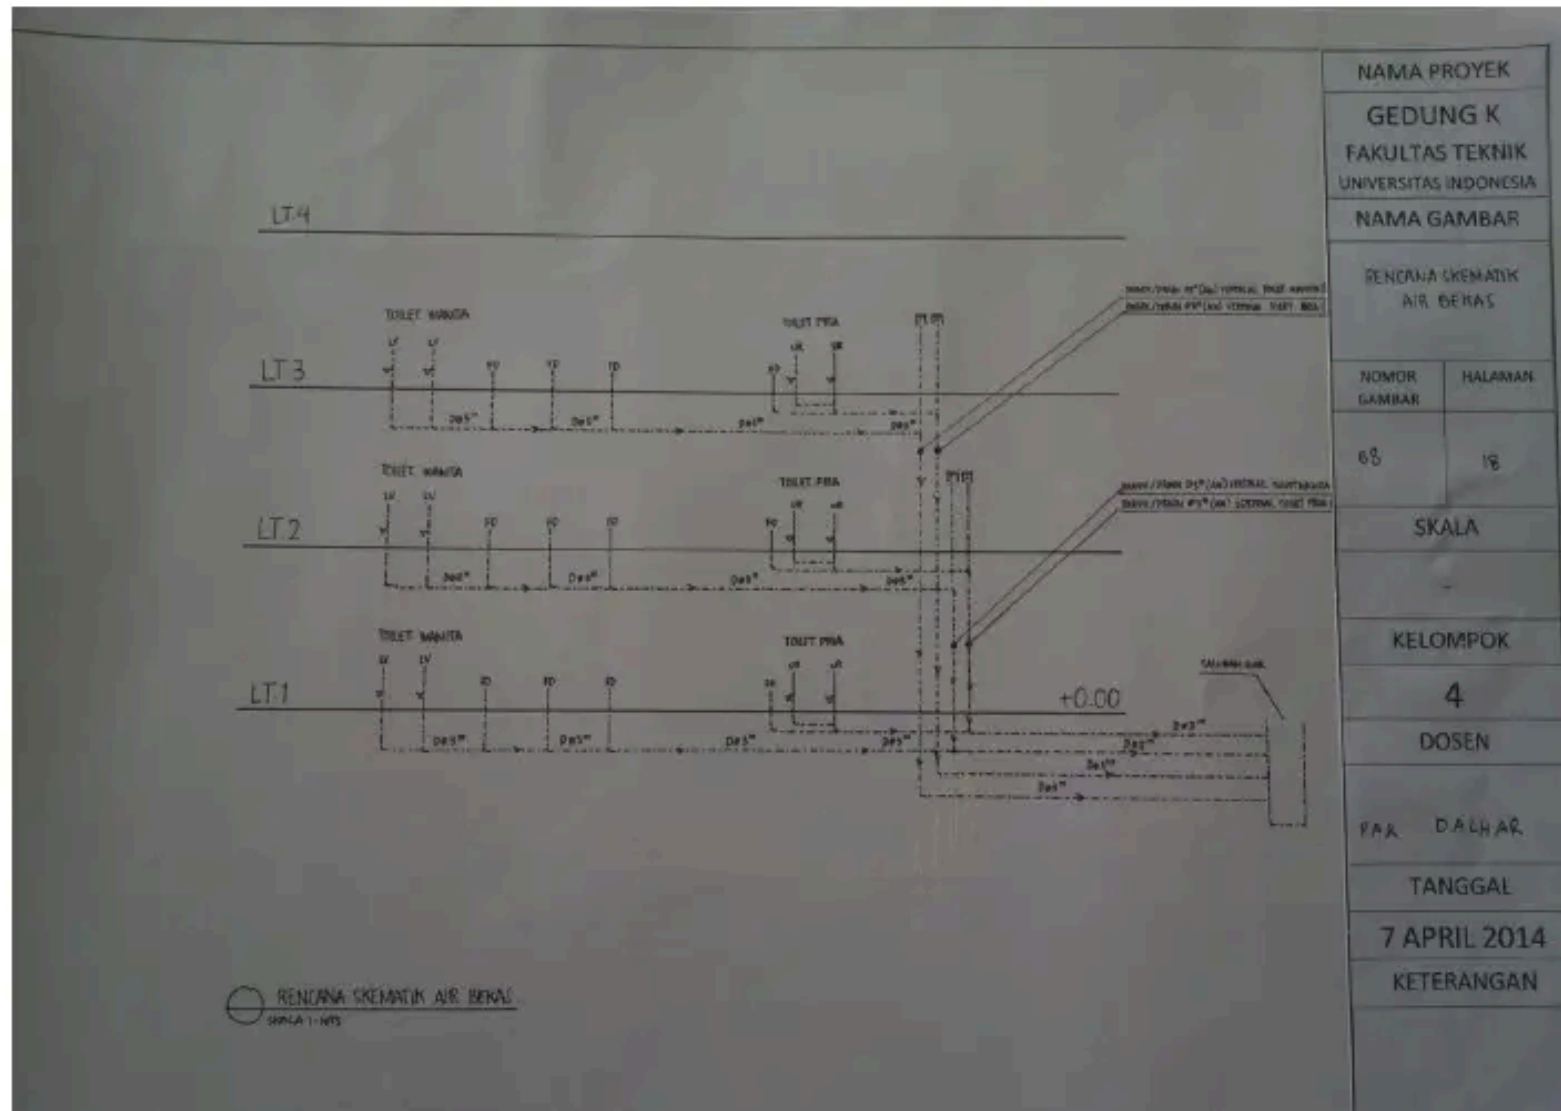

DENAH PEMIPAAN AIR BEKAS LANTAI DASAR

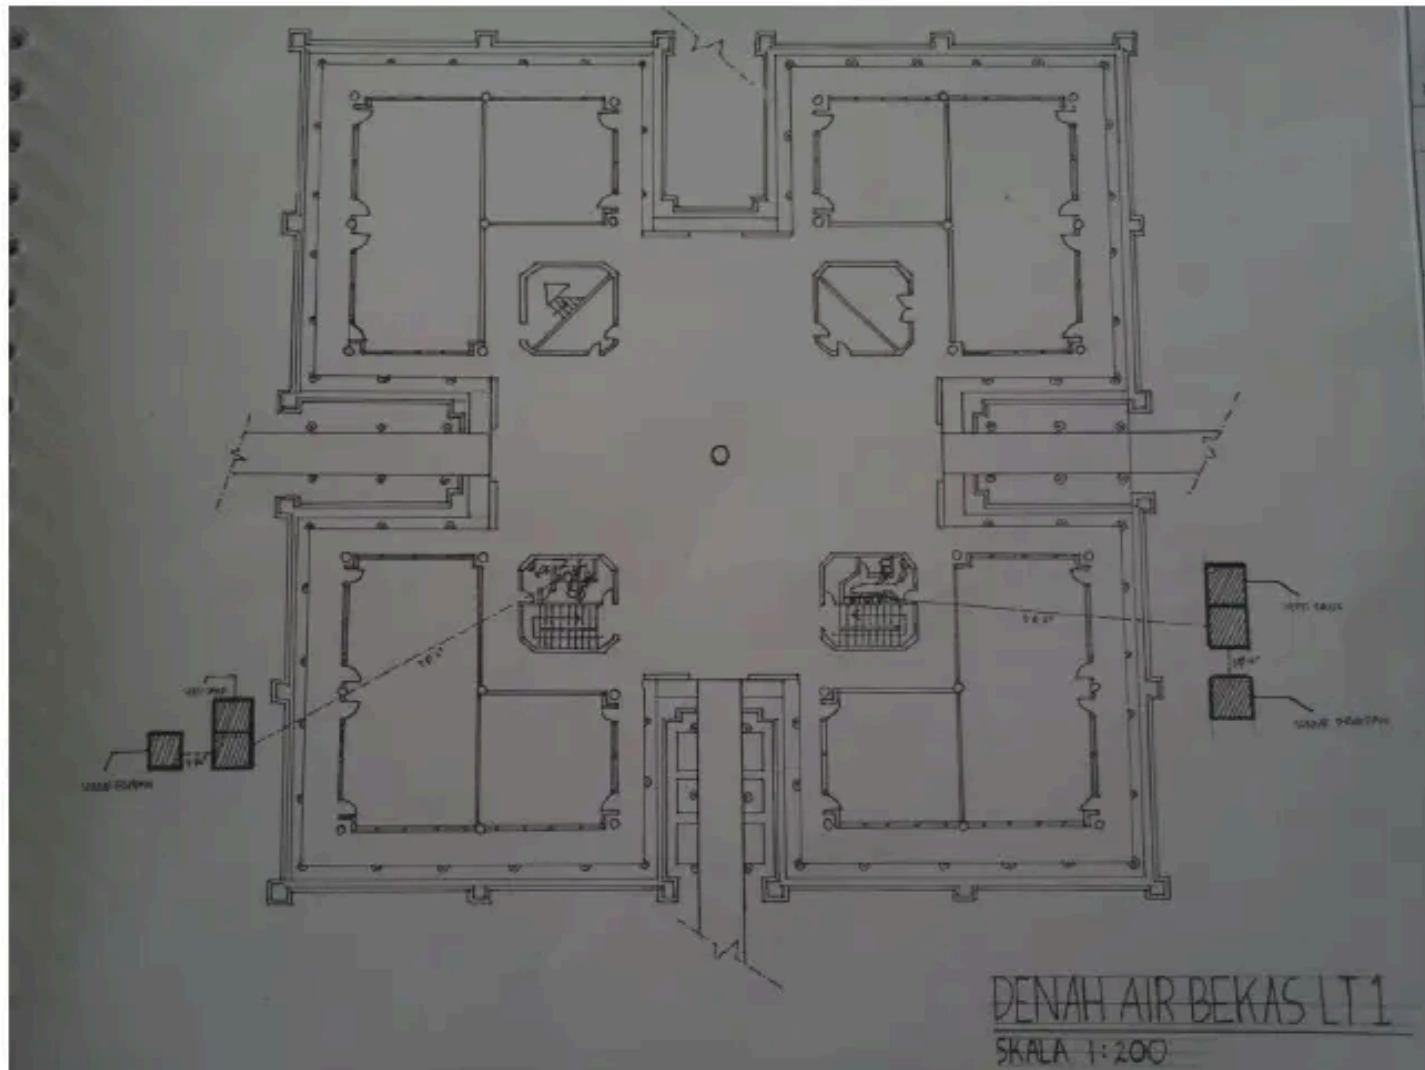

DENAH PEMIPAAN AIR BEKAS LANTAI 1-4 (TOILET WANITA)

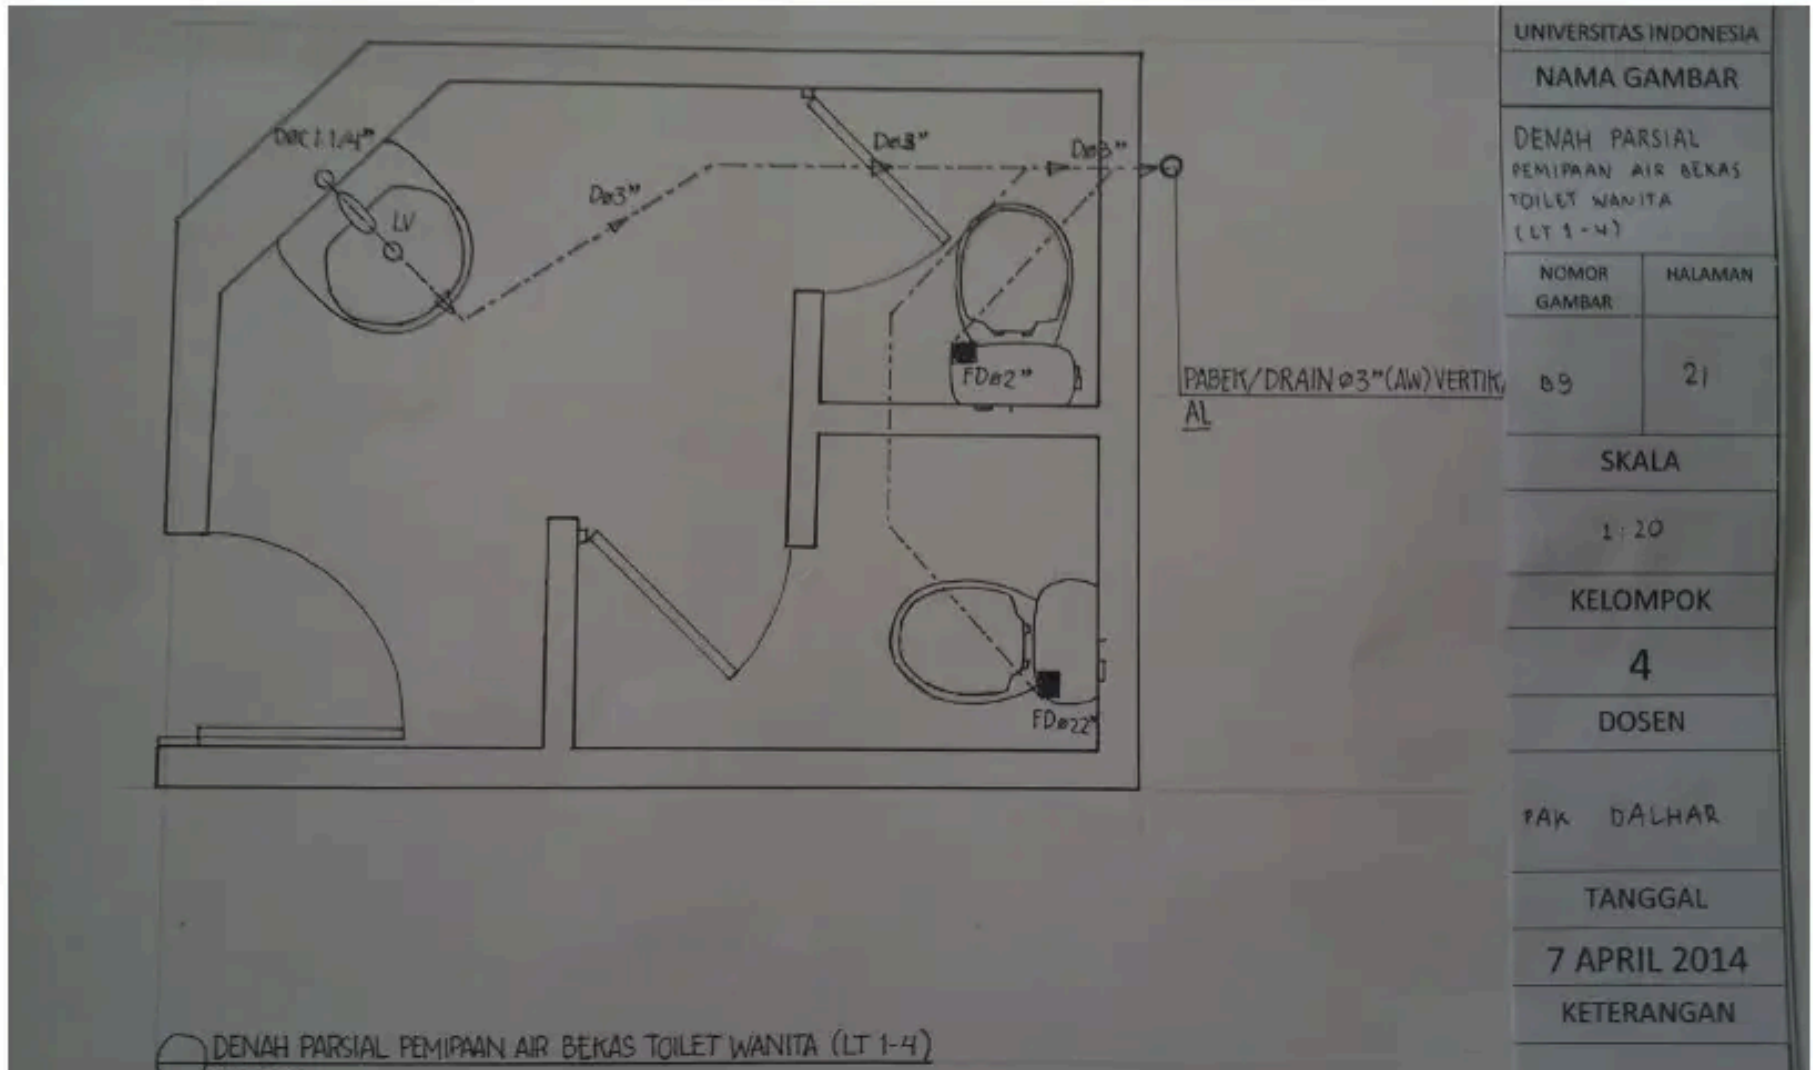

UNIVERSITAS INDONESIA

NAMA GAMBAR

DENAH PARSIAL
PEMIPAAN AIR BEKAS
TOILET WANITA
(LT 1-4)

NOMOR
GAMBAR

HALAMAN

09

21

SKALA

1 : 20

KELOMPOK

4

DOSEN

PAK DALHAR


TANGGAL

7 APRIL 2014

KETERANGAN

PABEK/DRAIN $\phi 3''$ (AW) VERTIKAL
AL

DENAH PEMIPAAN AIR BEKAS LANTAI 1-4 (TOILET PRIA)

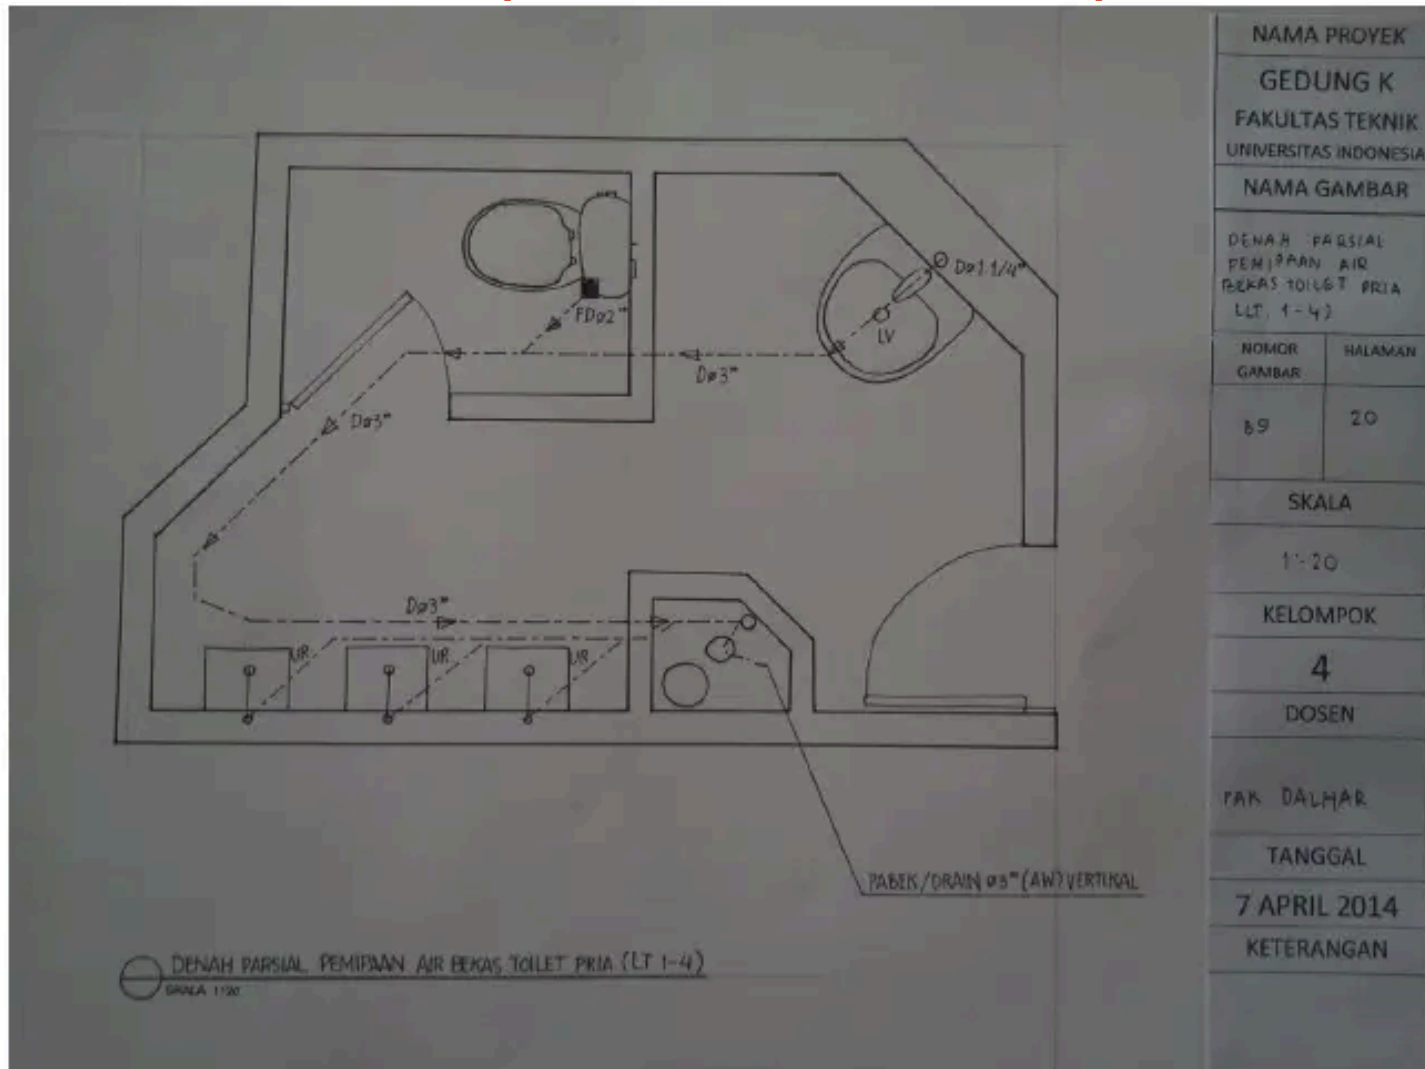

DENAH PEMIPAAN AIR BEKAS LANTAI 1-2 (PANTRY)



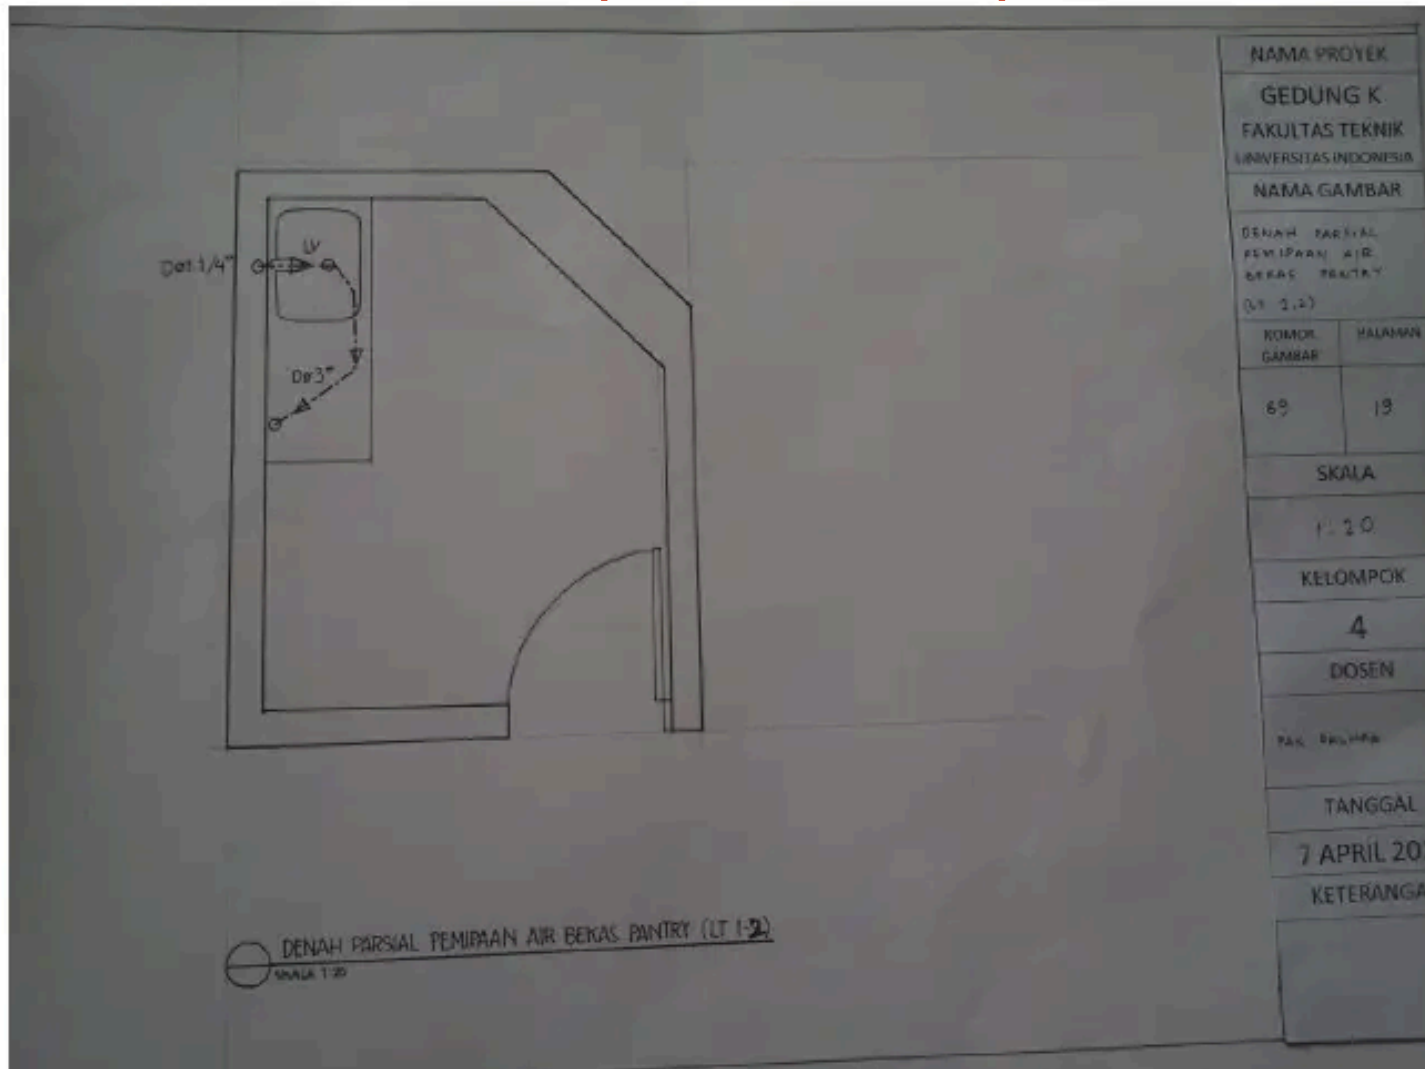



DIAGRAM SKEMATIK PEMIPAAN AIR KOTOR SATU GARIS

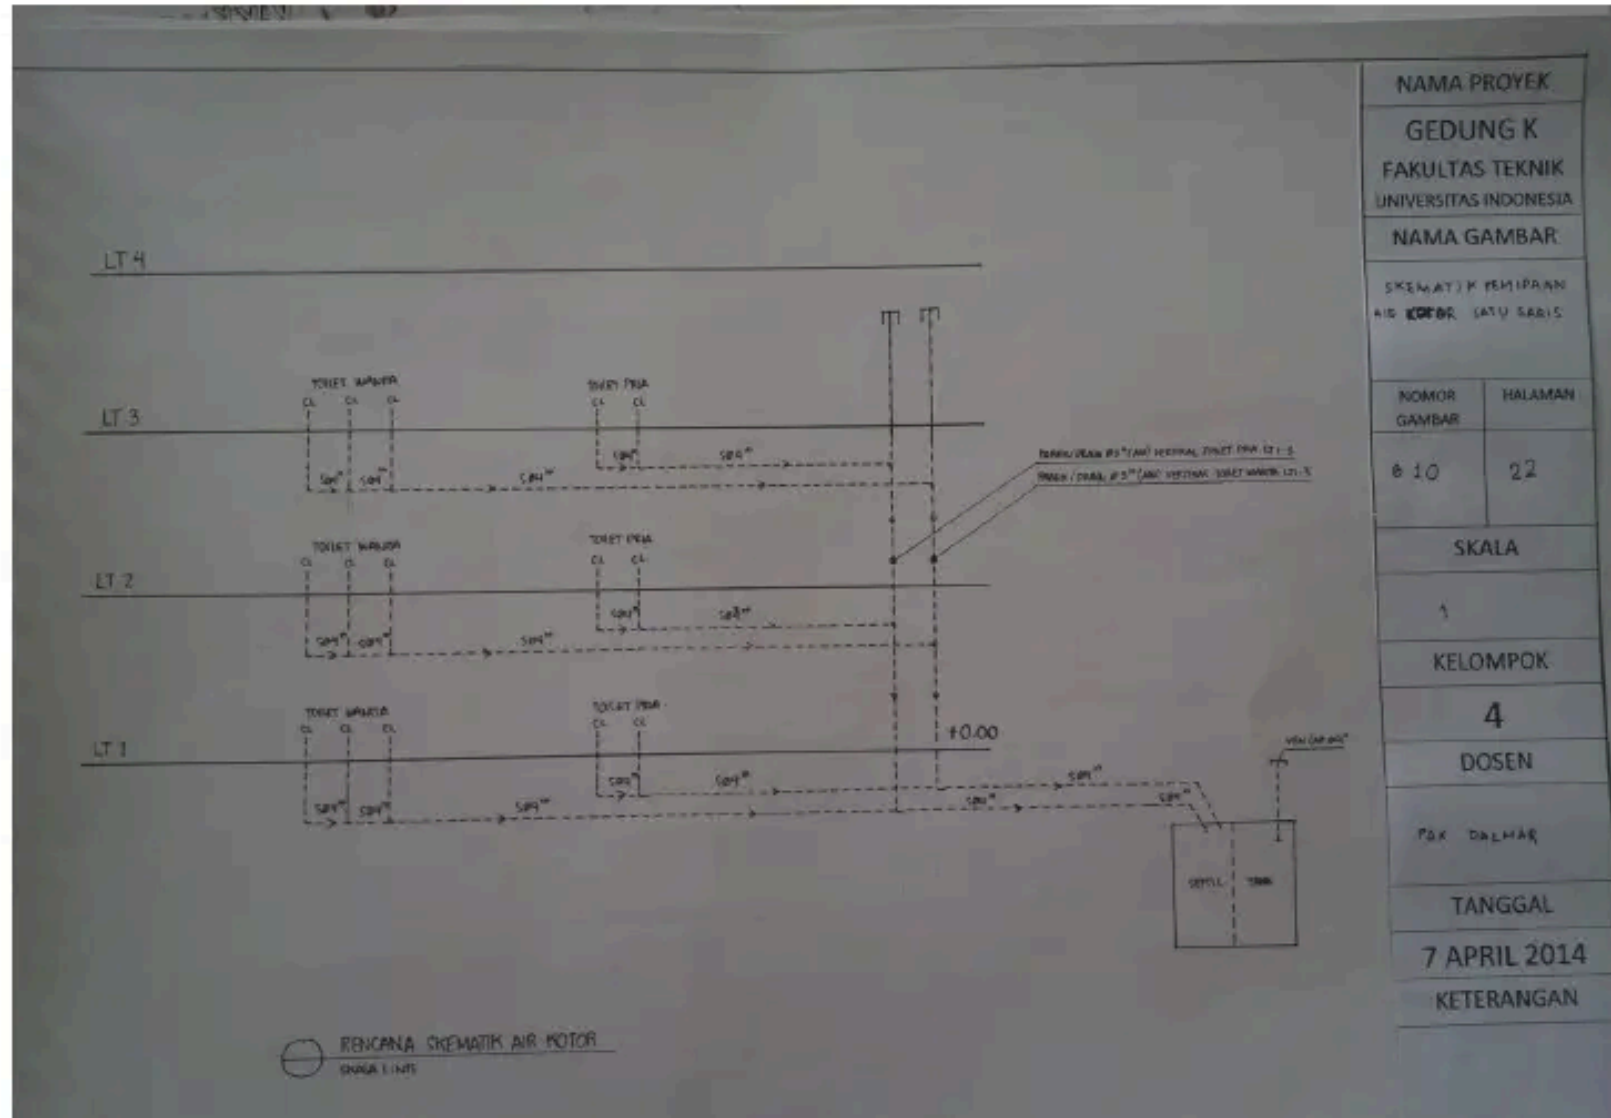


DENAH PEMIPAAN AIR KOTOR LANTAI DASAR

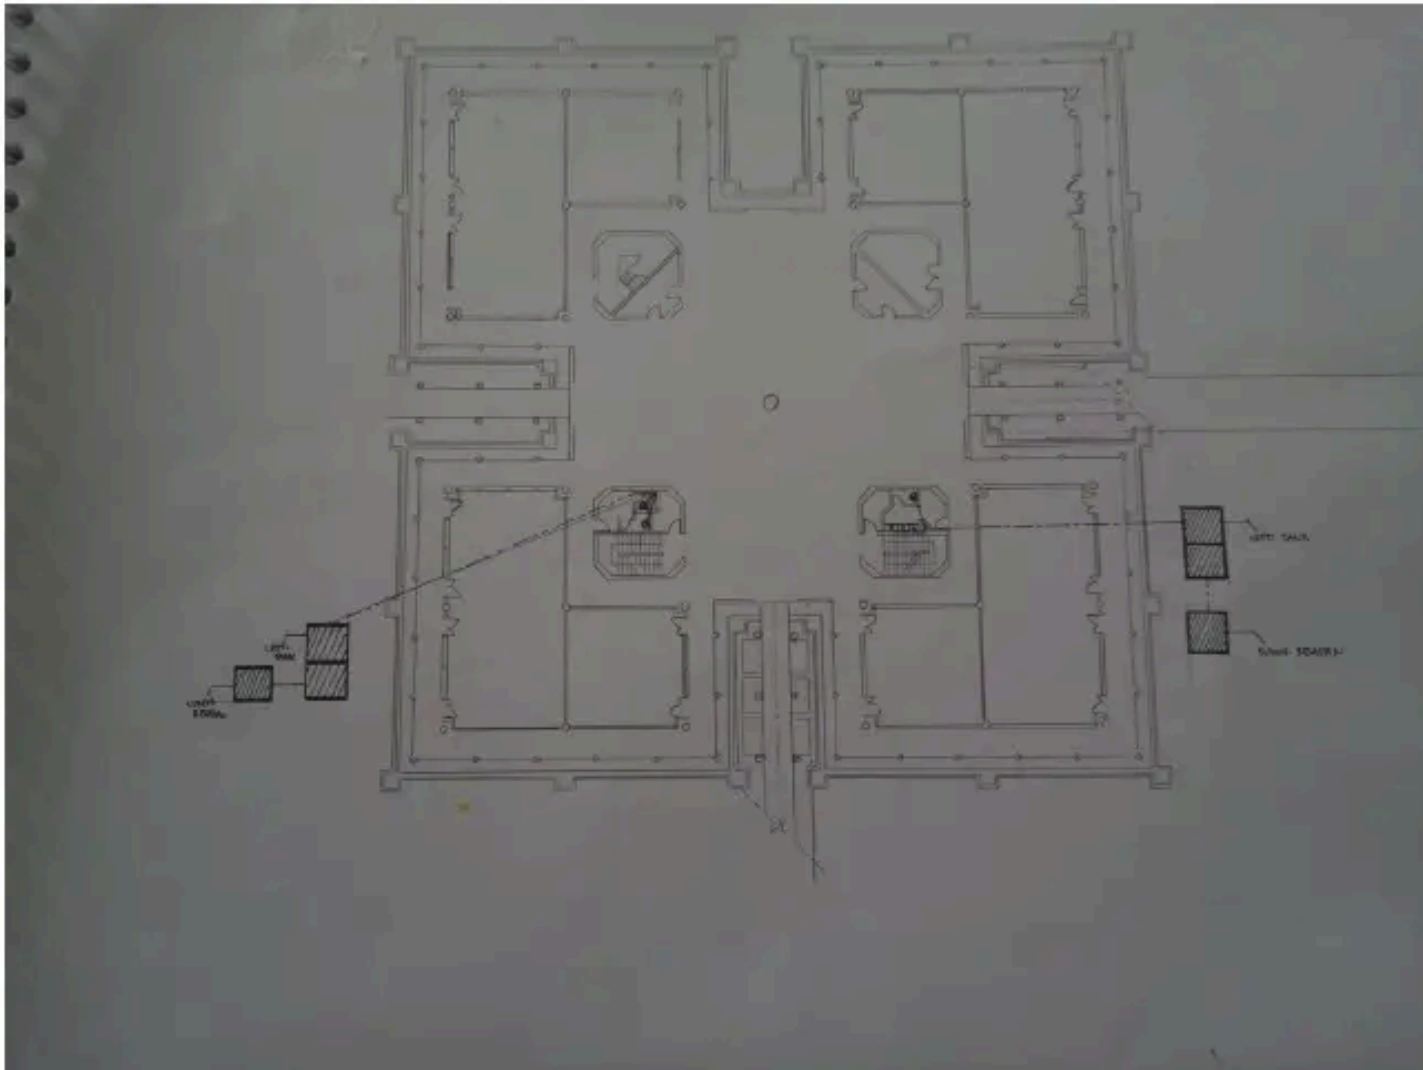


DENAH PEMIPAAN AIR KOTOR LANTAI 1-4 (TOILET PEREMPUAN)

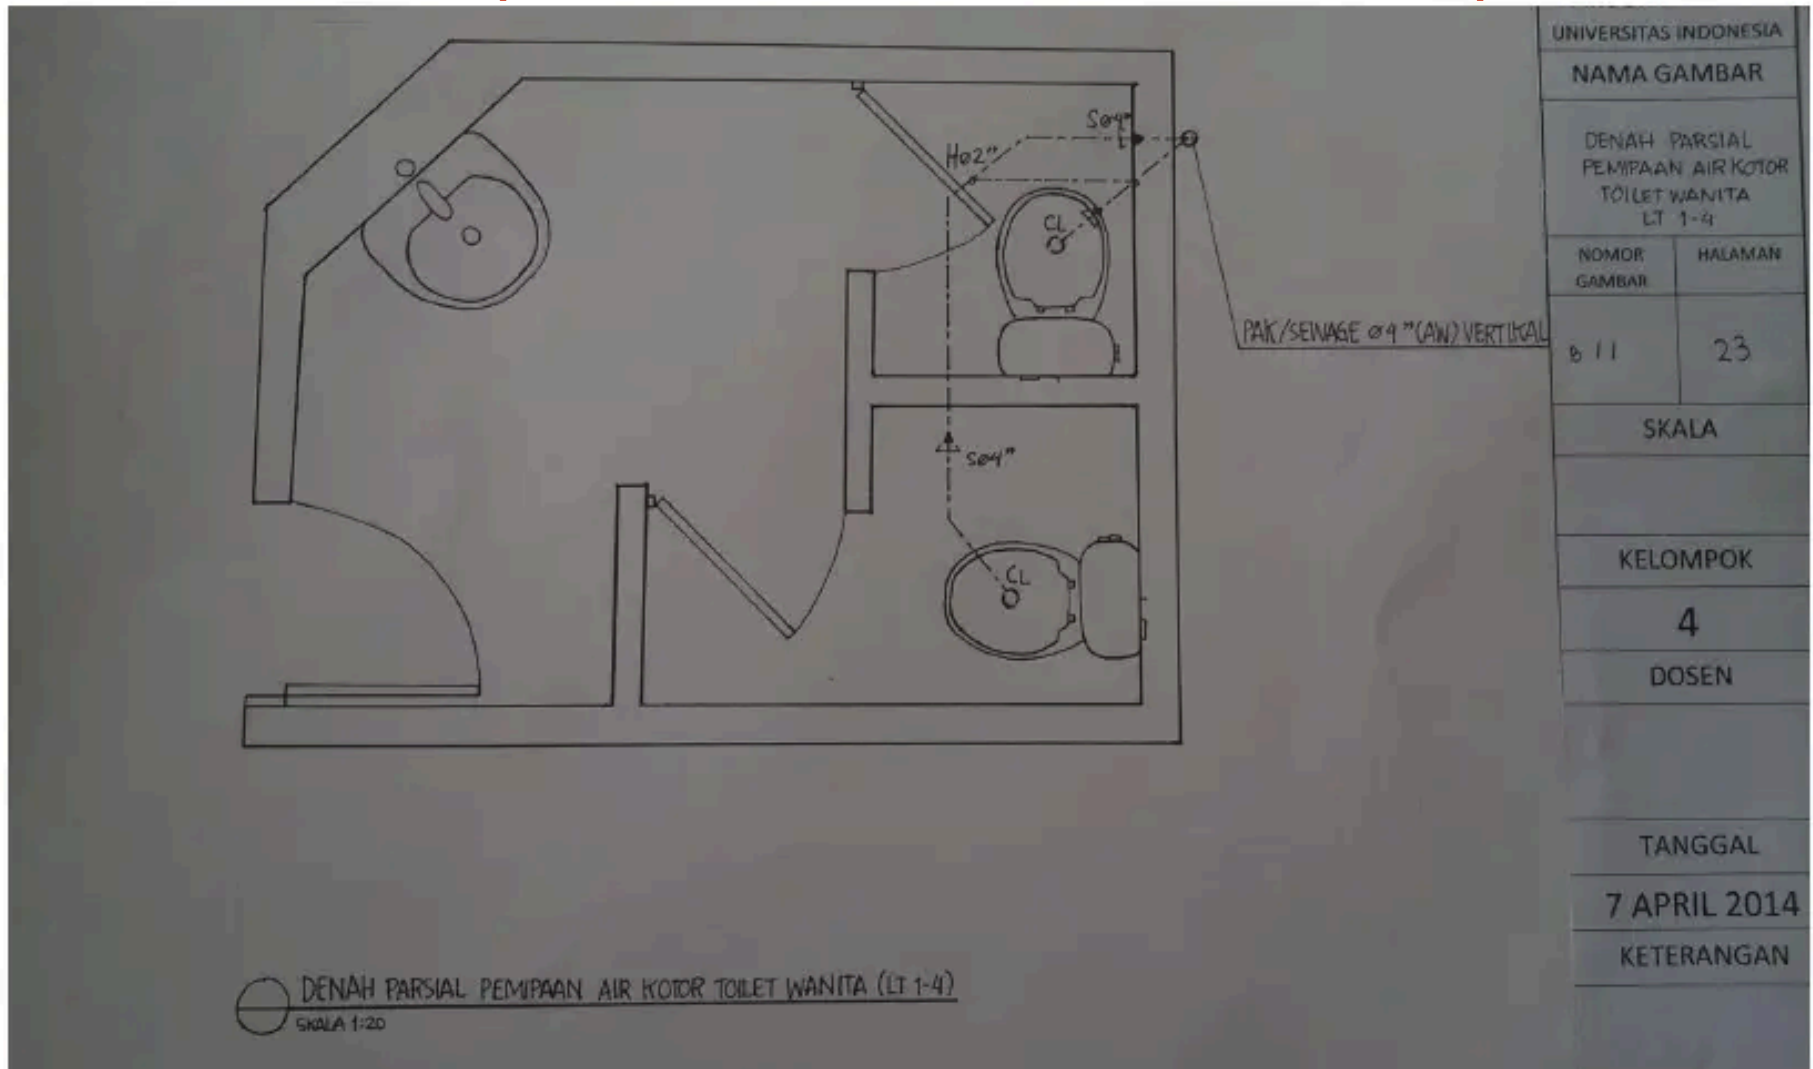


DENAH PEMIPAAN AIR KOTOR LANTAI 1-4 (TOILET PRIA)

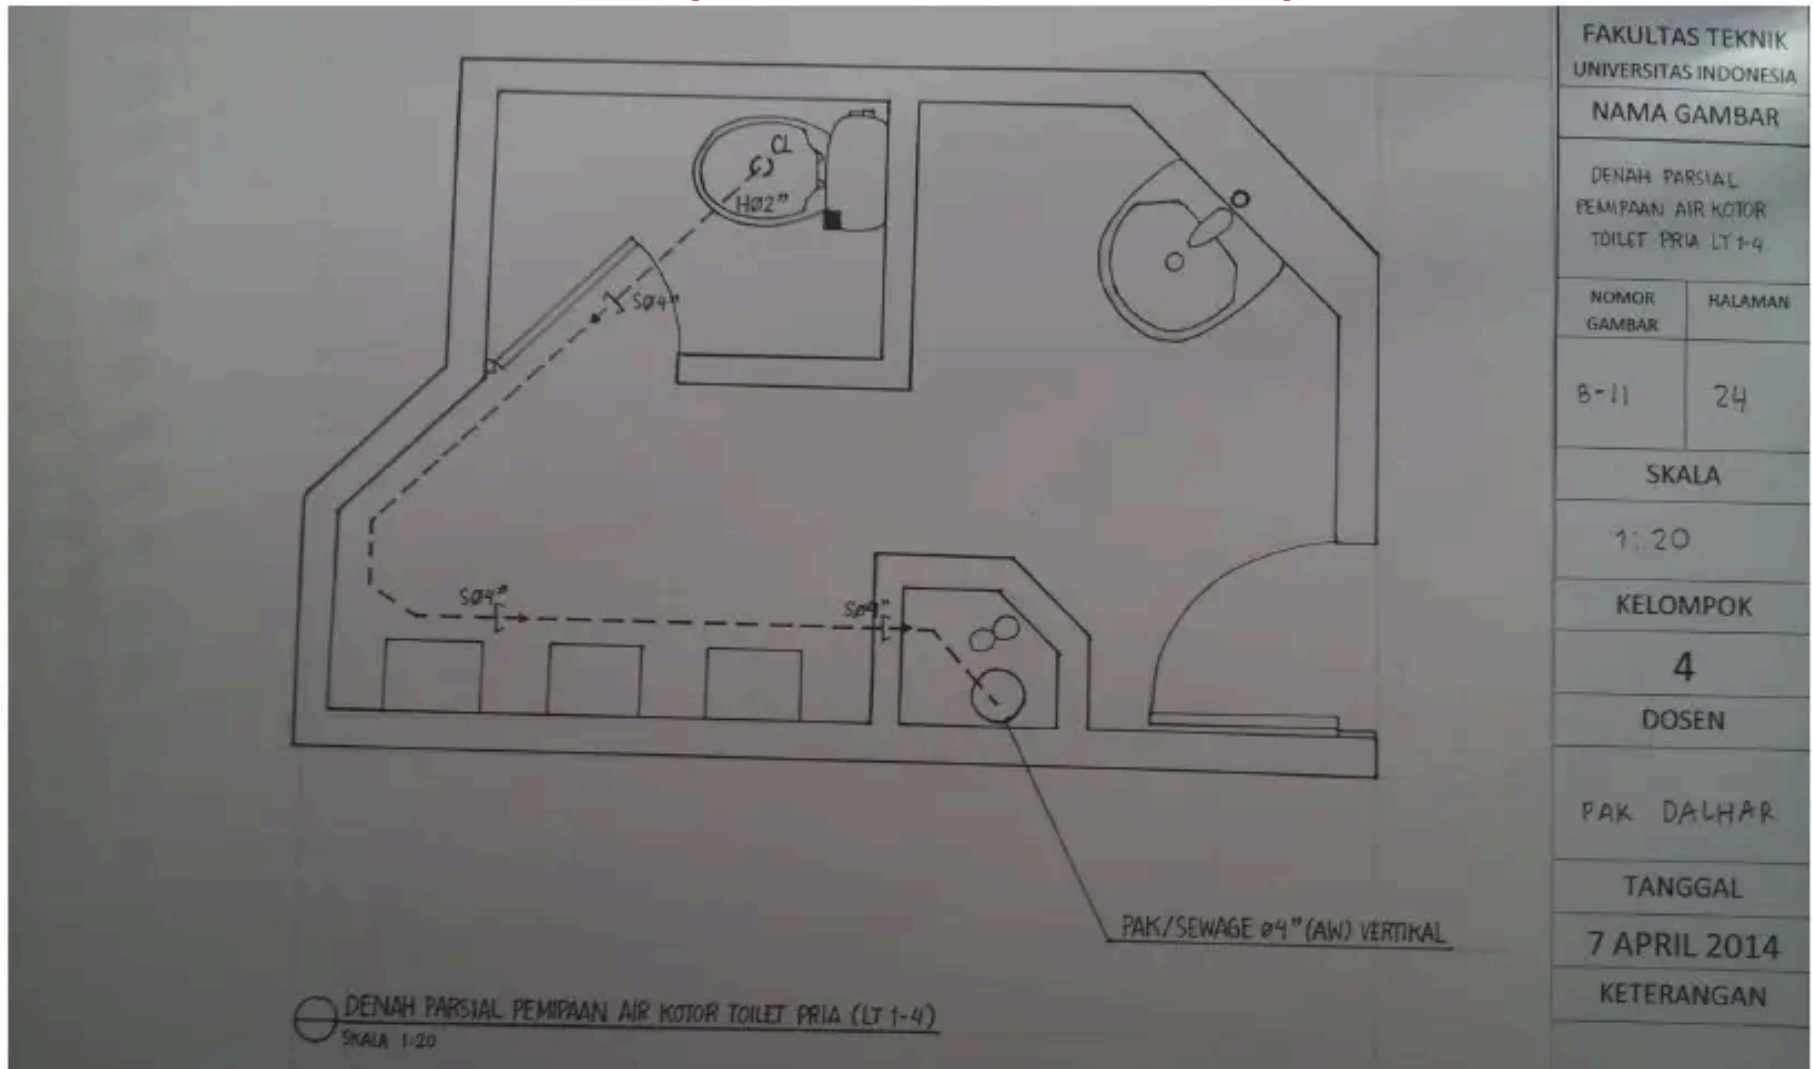

DETAIL SEPTIC TANK DAN SUMUR RESAPAN

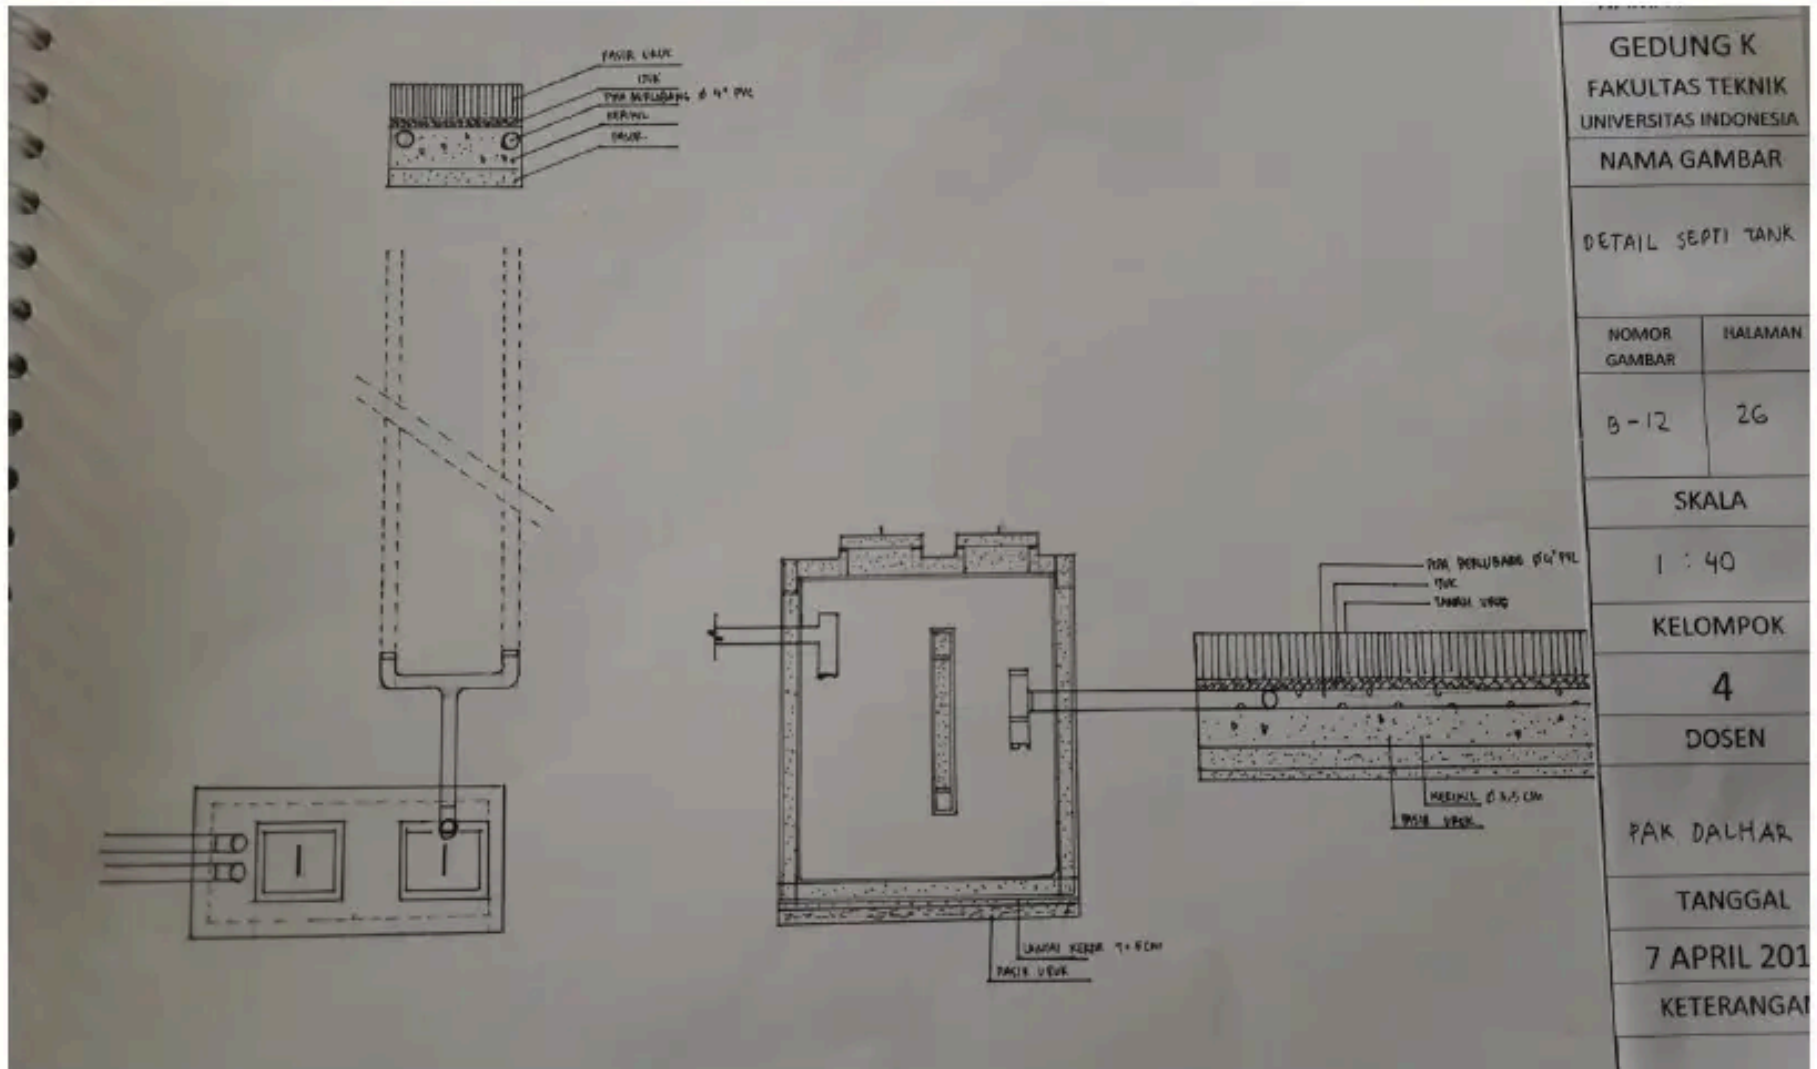

DETAIL SEPTIC TANK DAN SUMUR RESAPAN

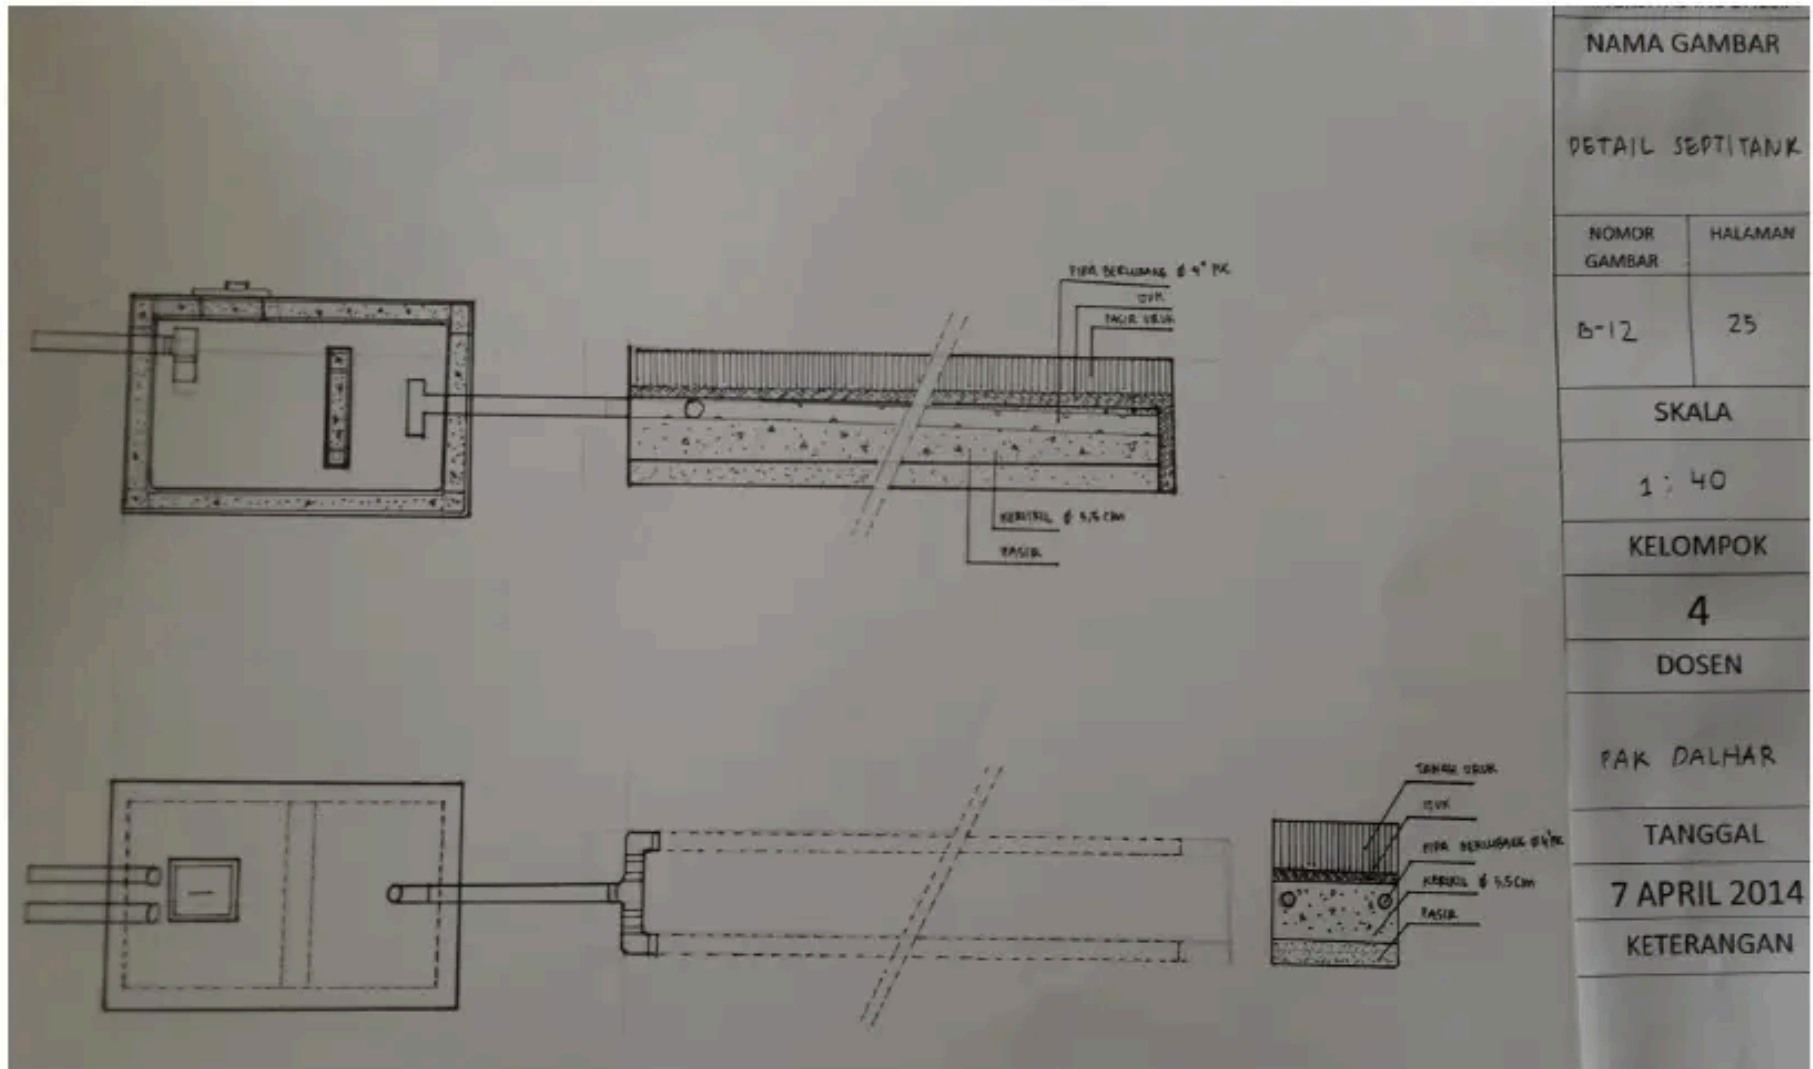

NAMA GAMBAR

DETAIL SEPTITANK

NOMOR
GAMBAR

HALAMAN

B-12

25

SKALA

1 : 40

KELOMPOK

4

DOSEN

PAK DALHAR

TANGGAL


7 APRIL 2014

KETERANGAN


PLUMBING

AIR HUJAN


ISOMETRIK PEMIPAAN AIR HUJAN

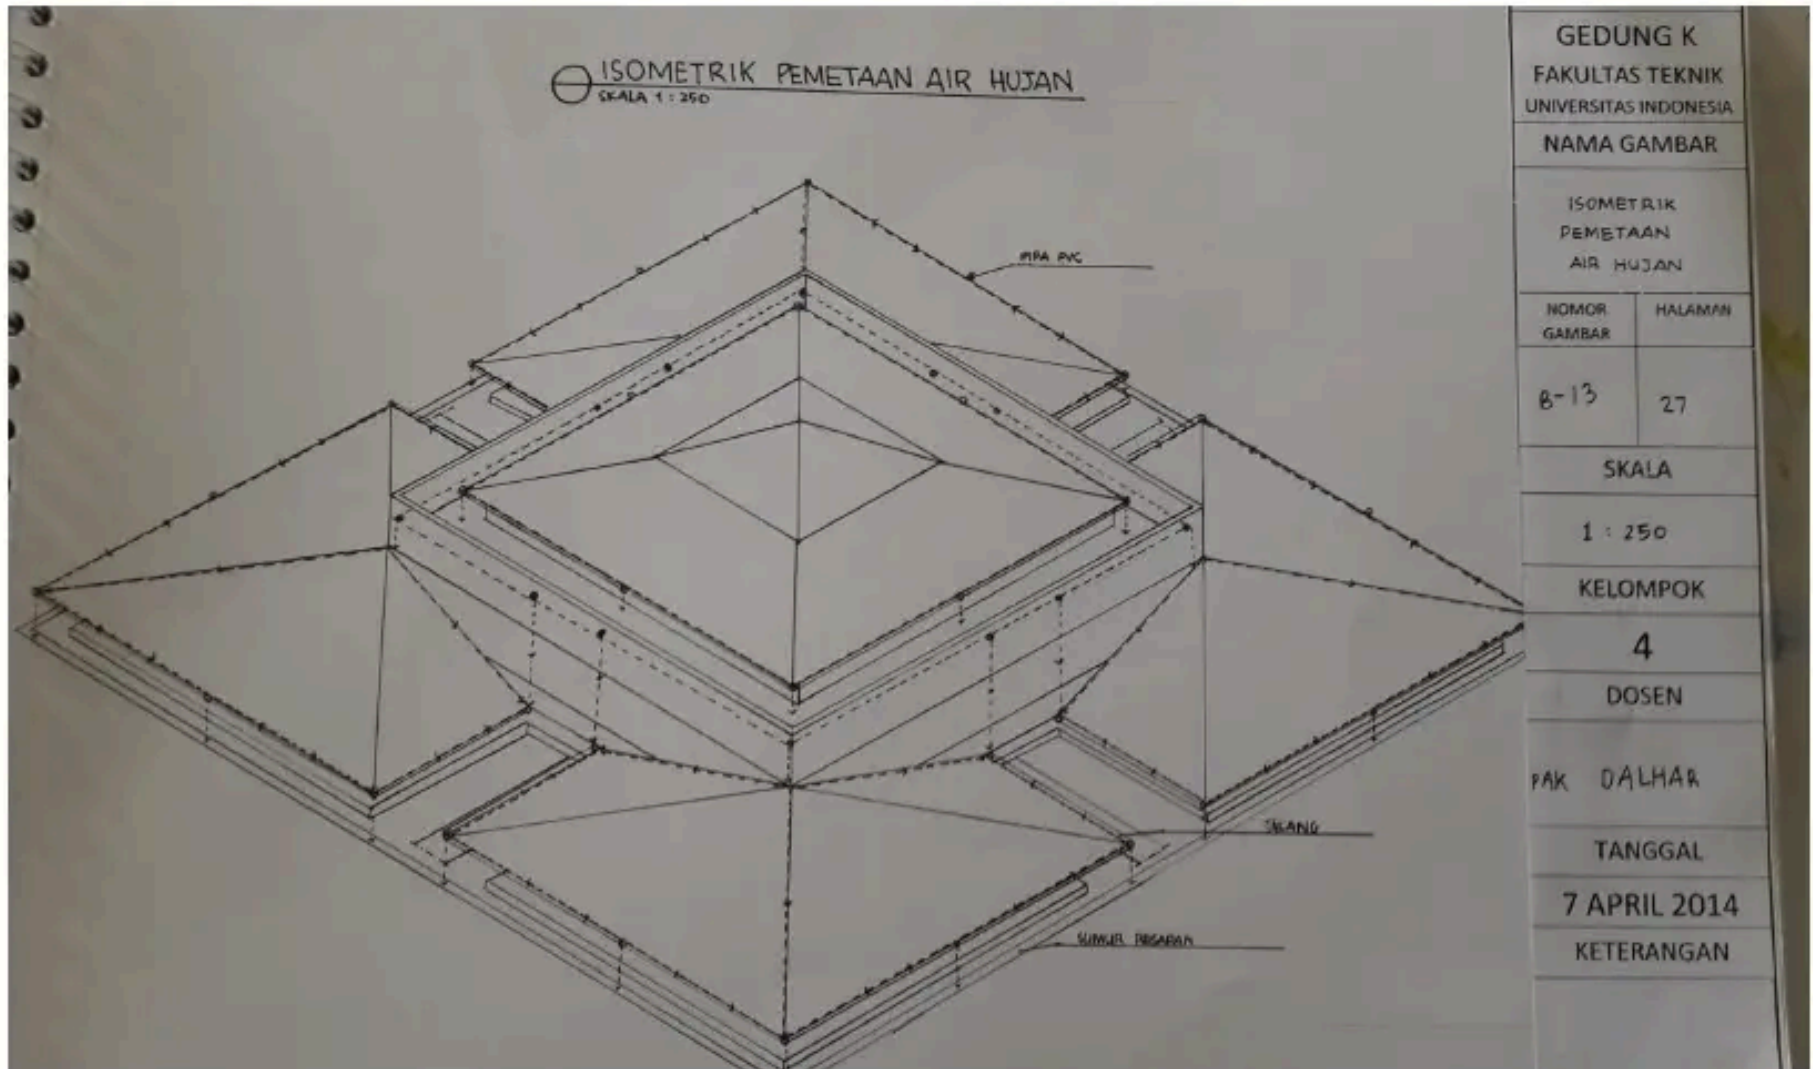


DENAH PEMIPAAN AIR HUJAN LANTAI DASAR

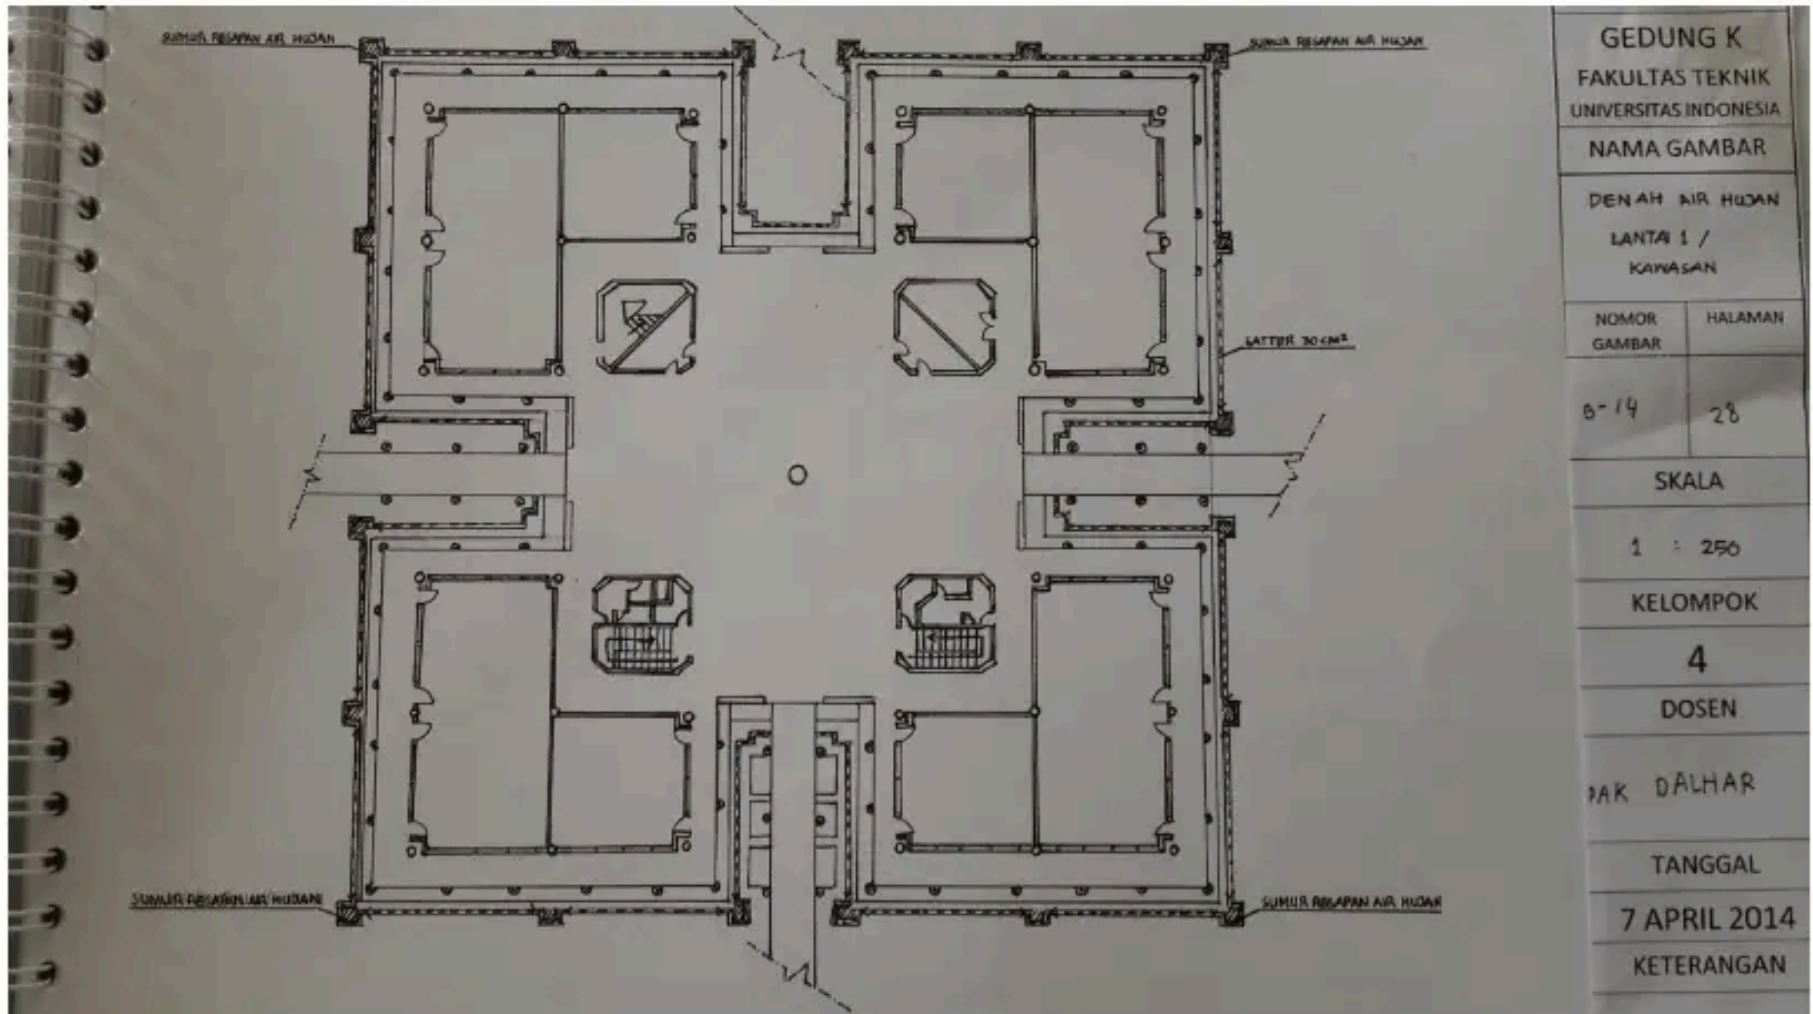


DENAH PEMIPAAN AIR HUJAN LANTAI 3 DAN ATAP

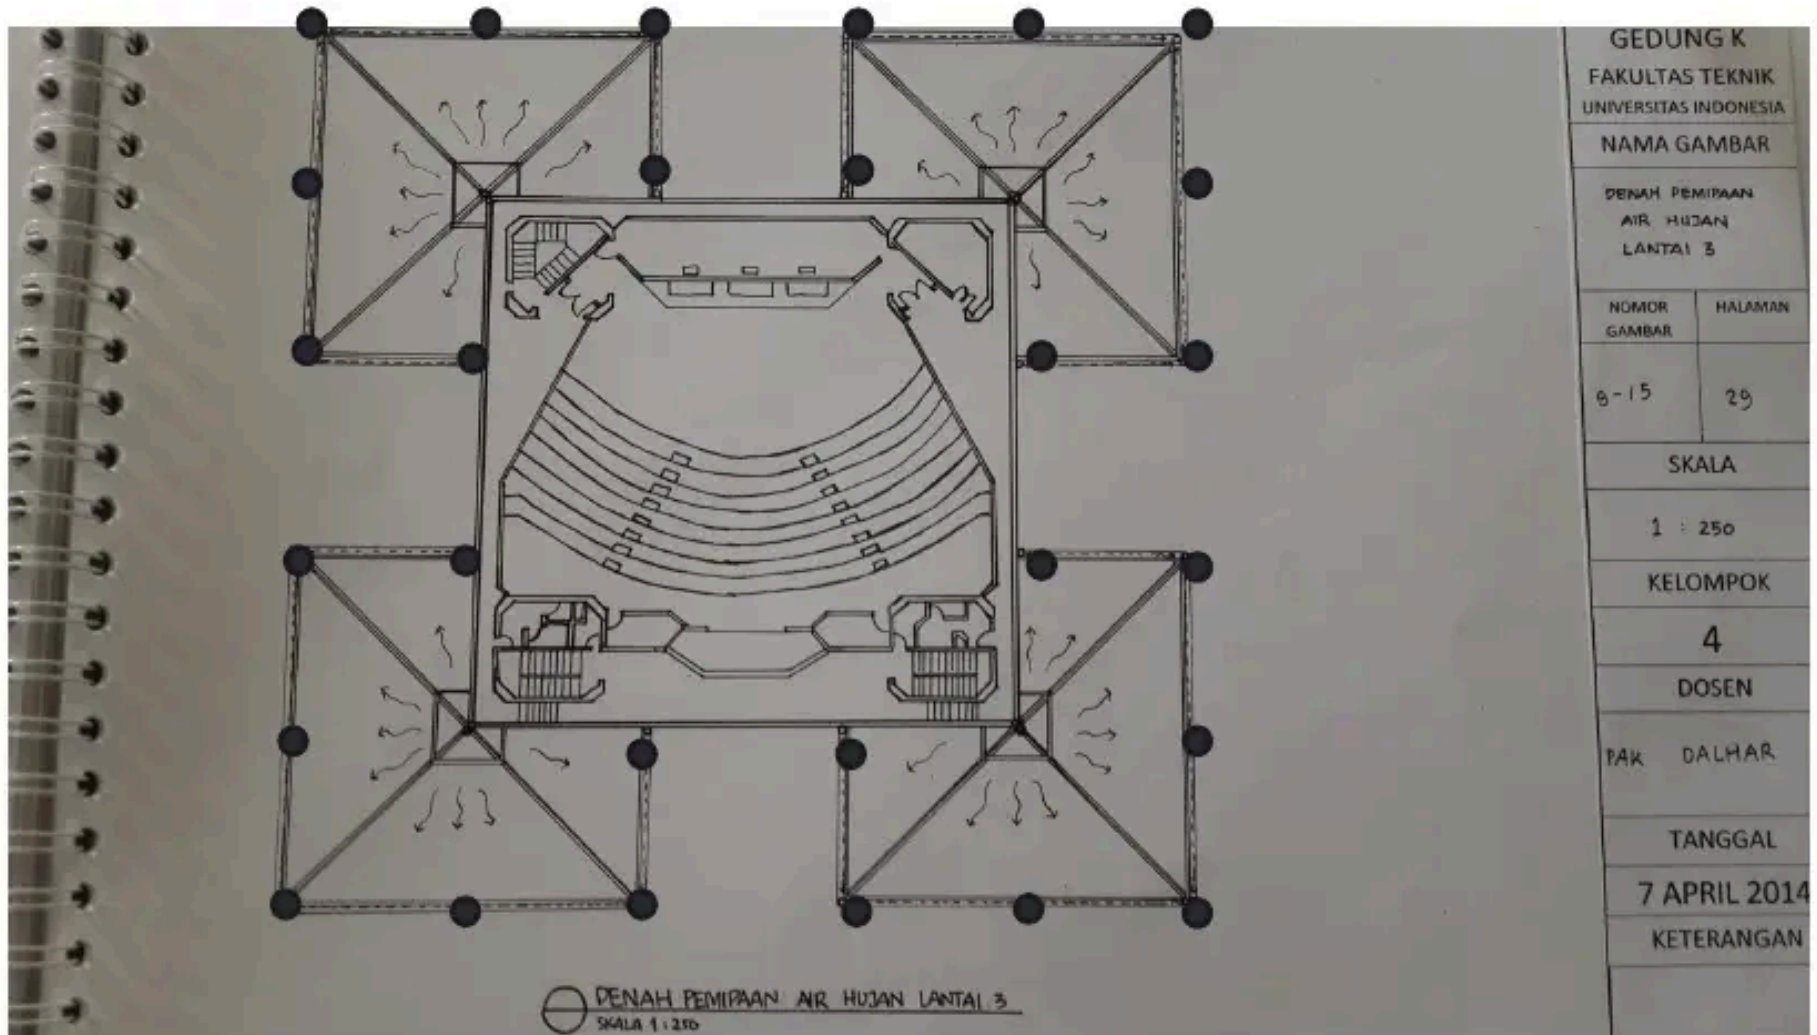


DENAH PEMIPAAN AIR HUJAN LANTAI ATAP

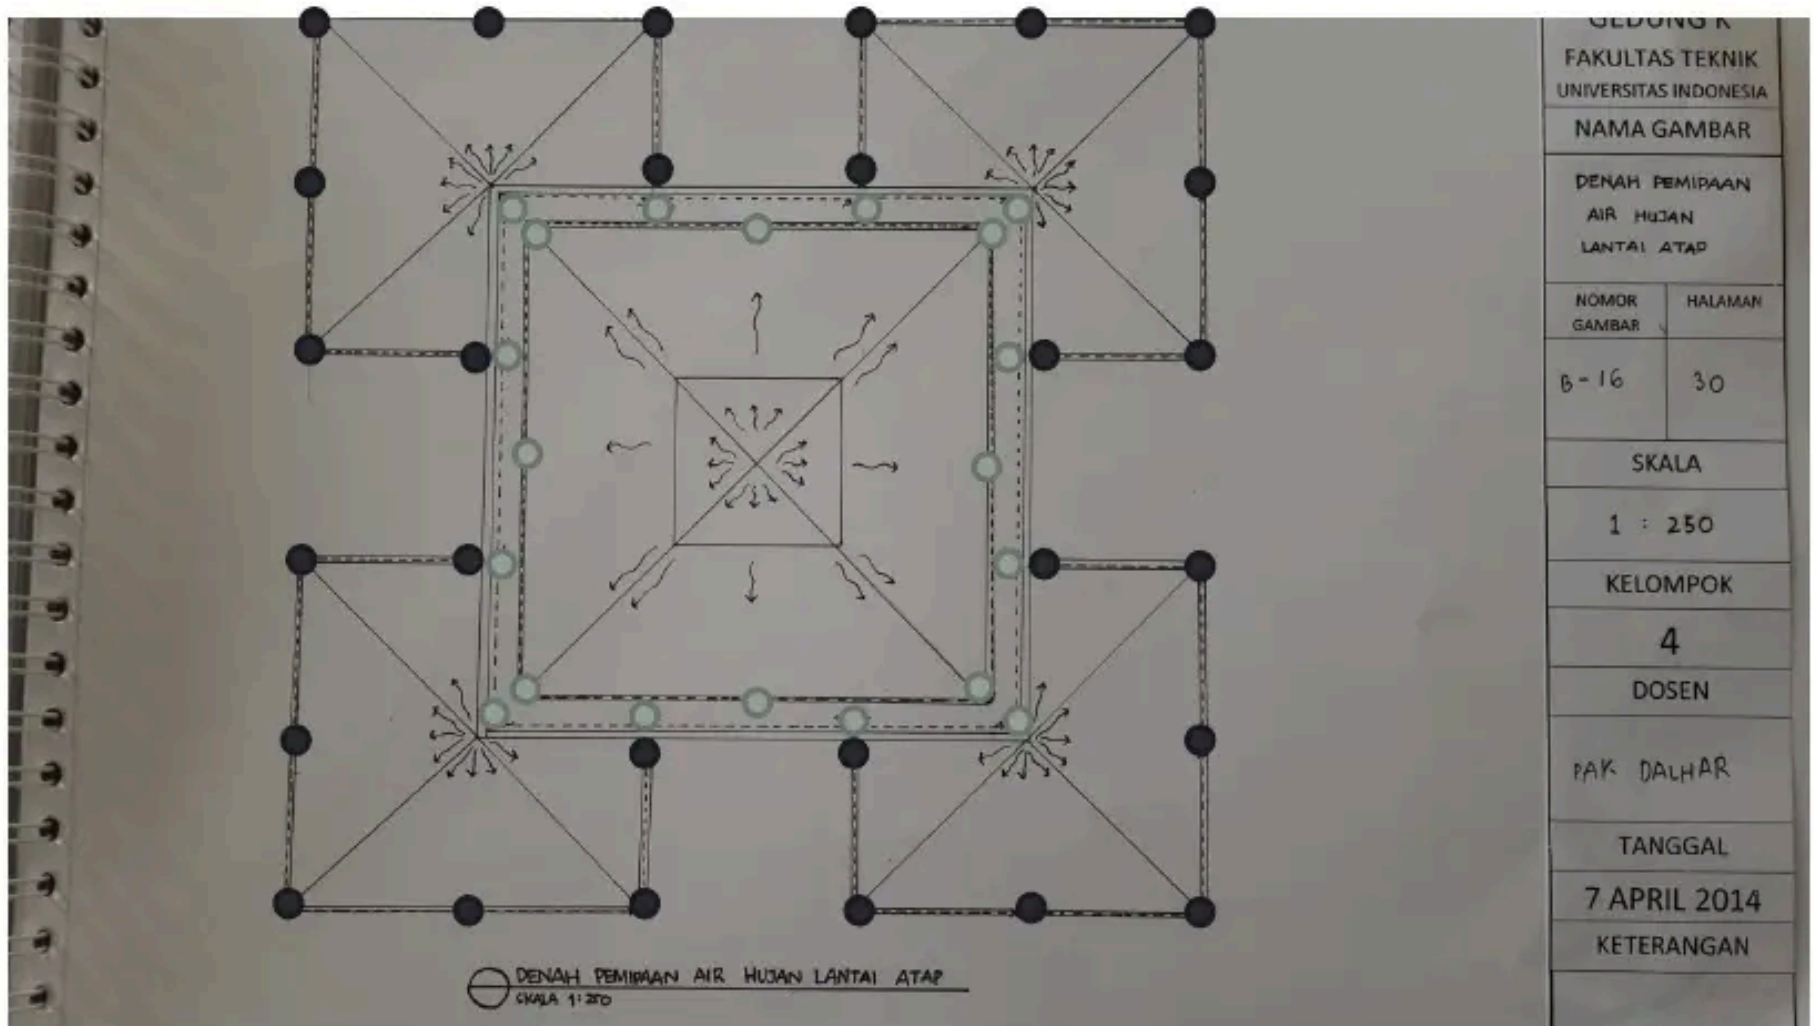

DETAIL TALANG

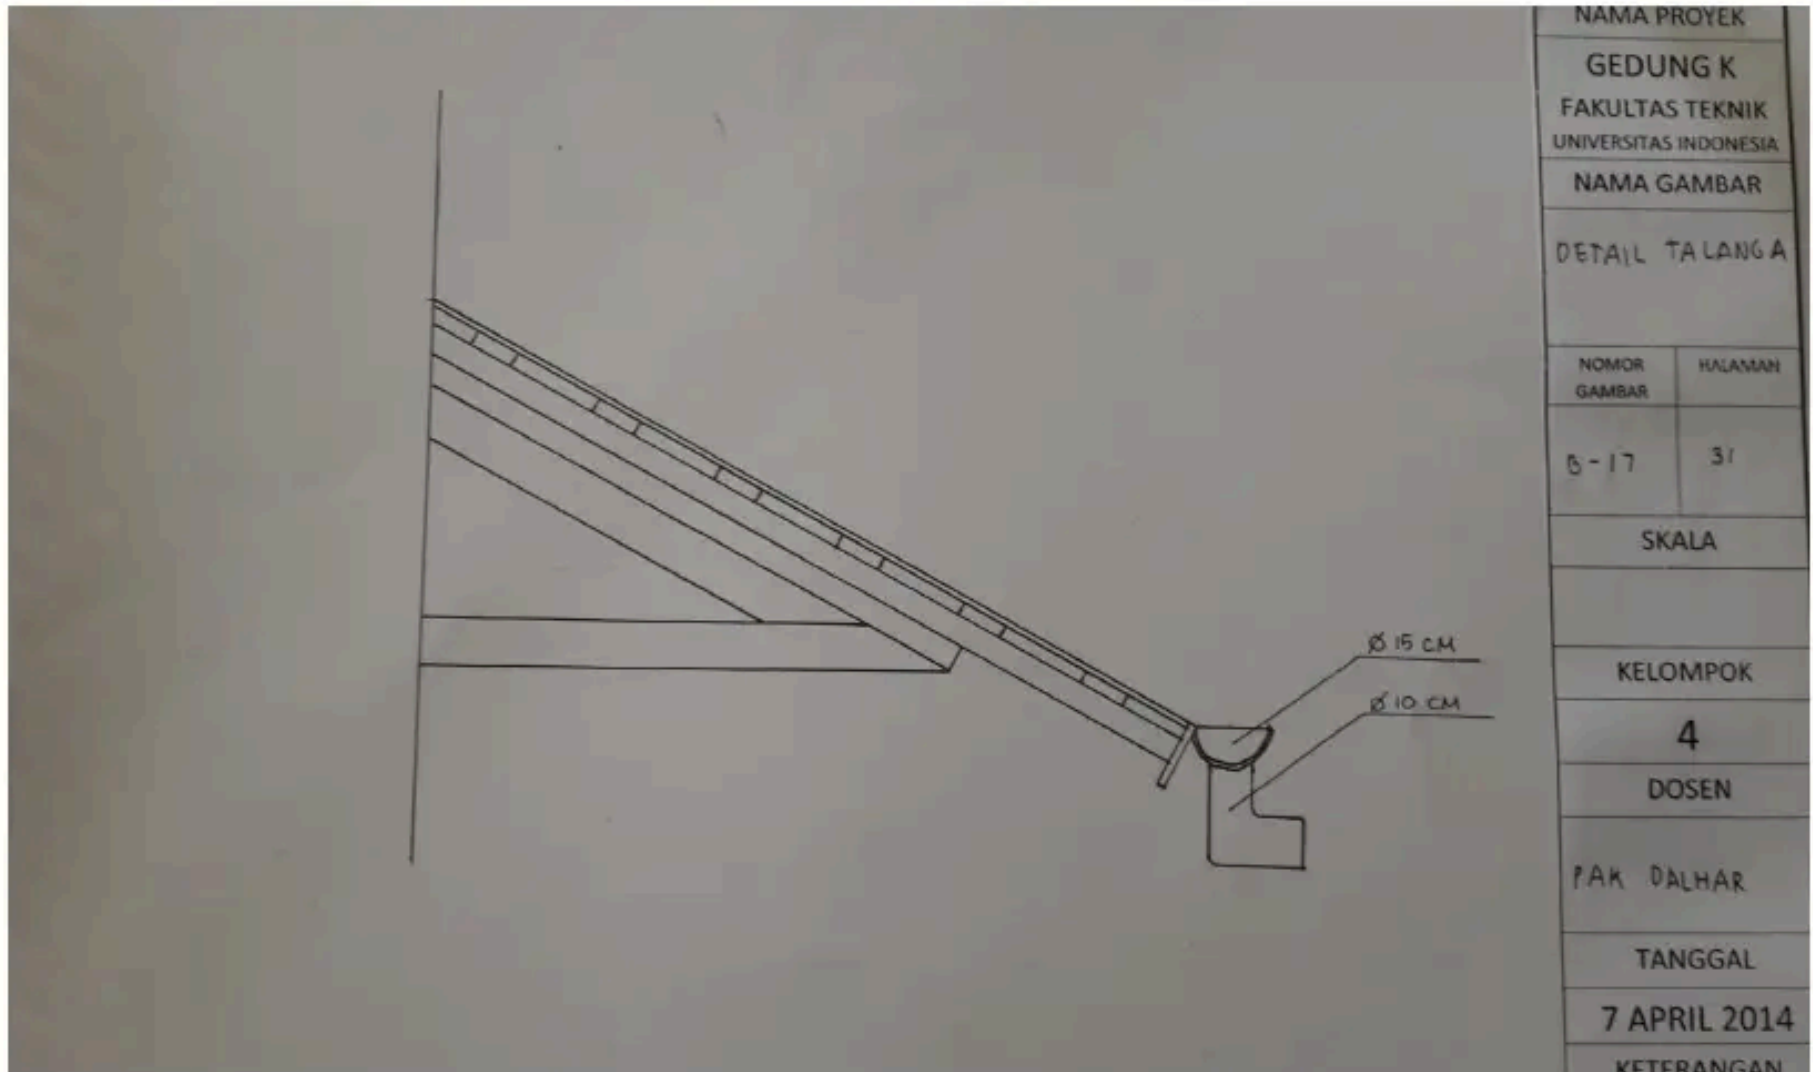


DETAIL TALANG

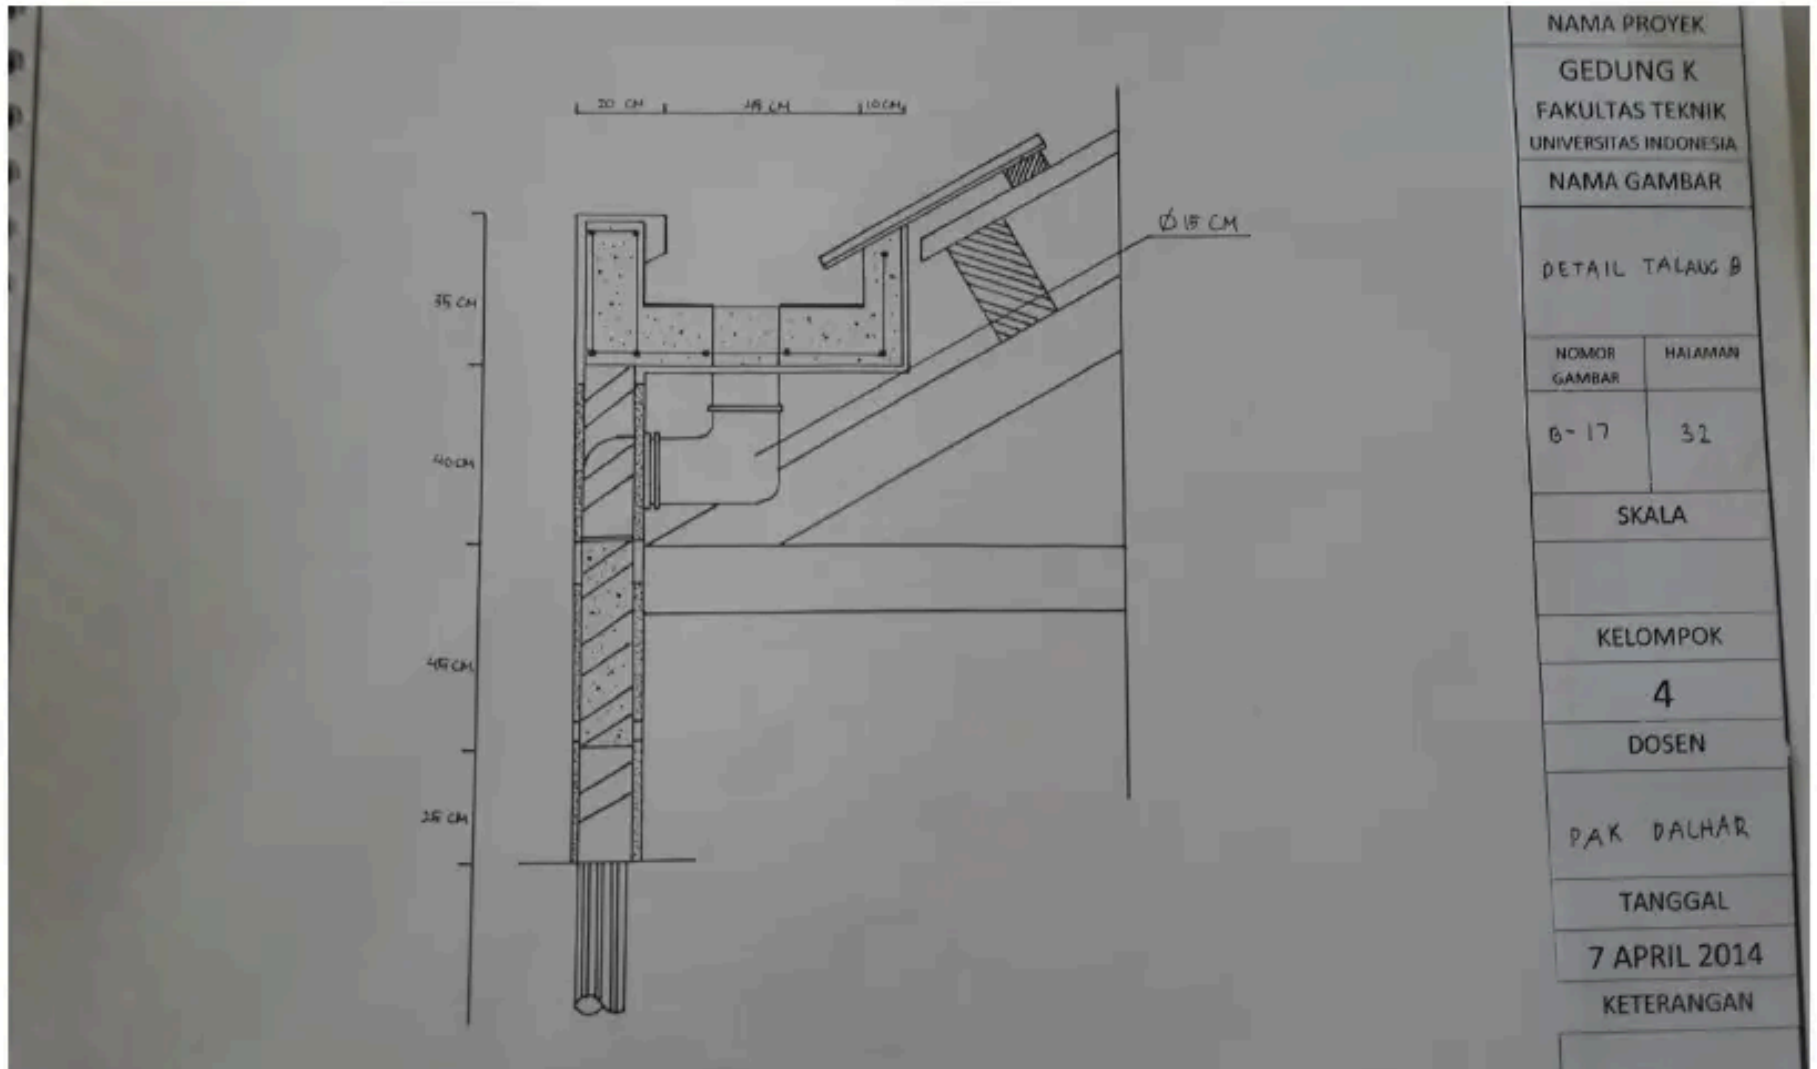


ELEKTRIKAL


DIAGRAM DISTRIBUSI DAYA LISTRIK

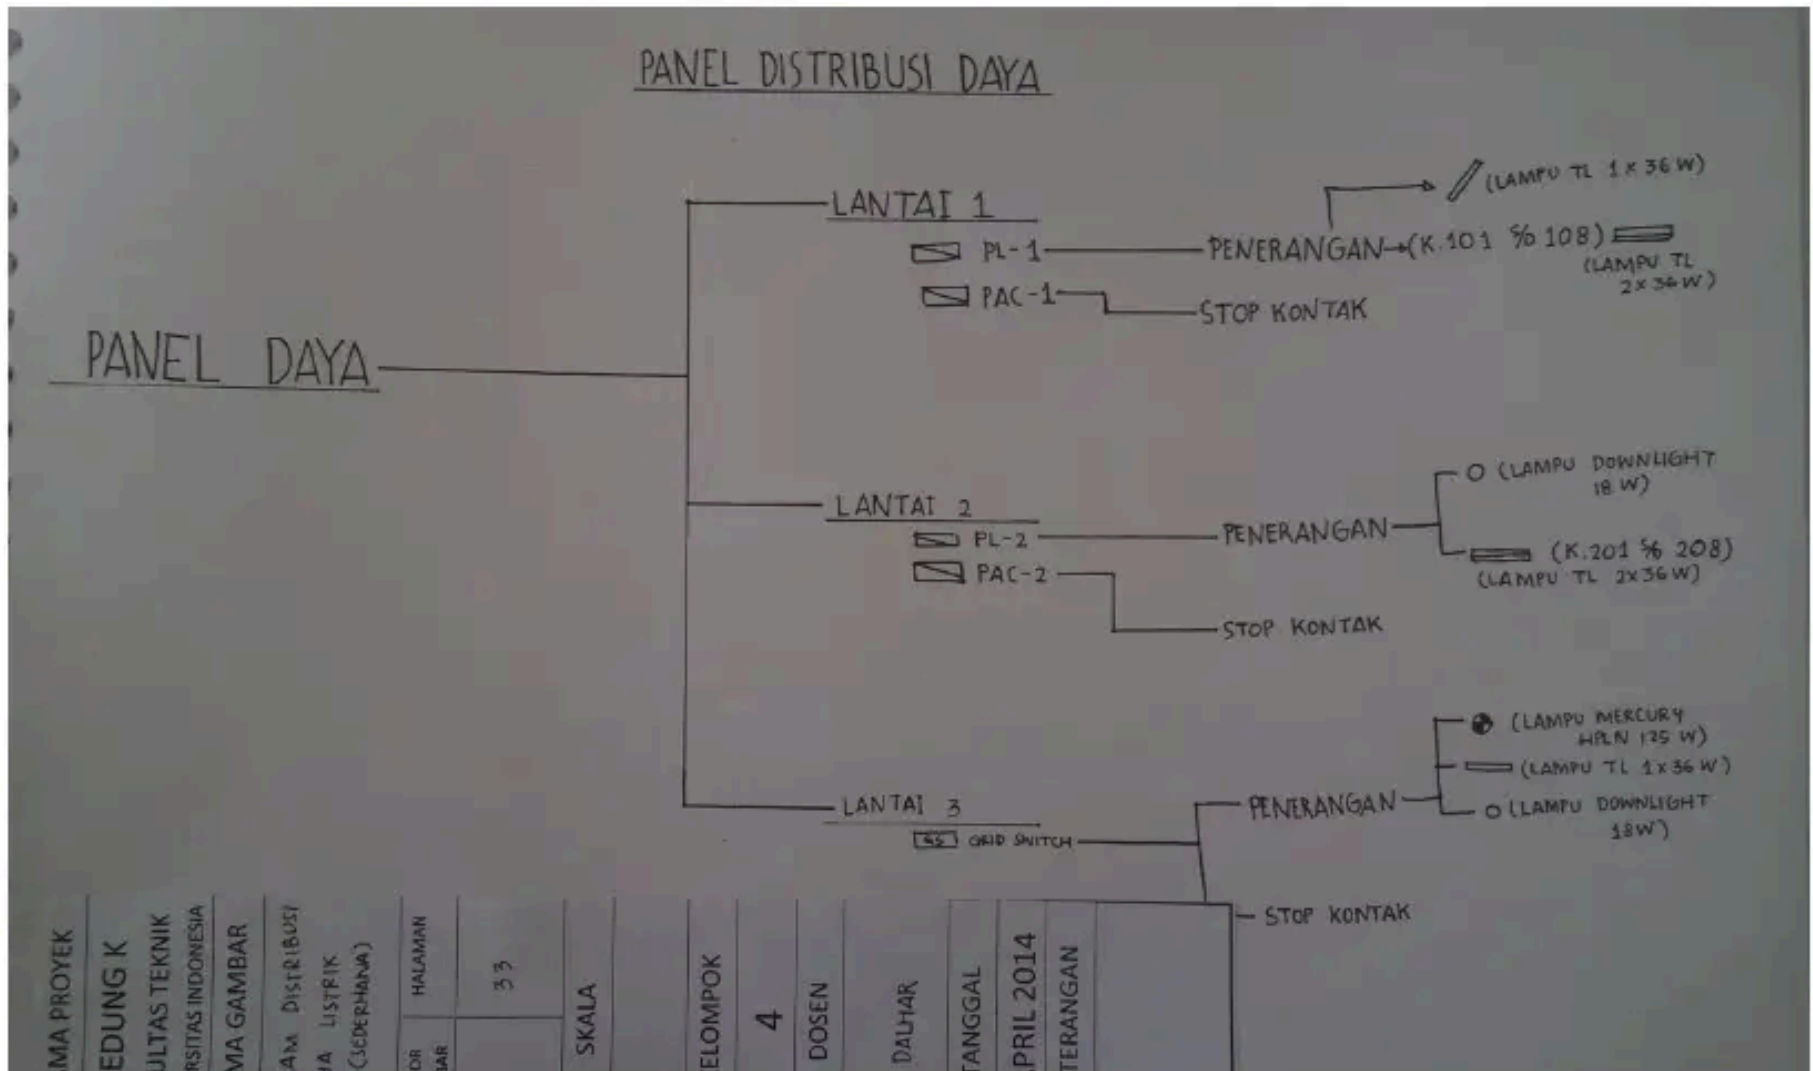


DENAH INSTALASI LISTRIK LANTAI 1

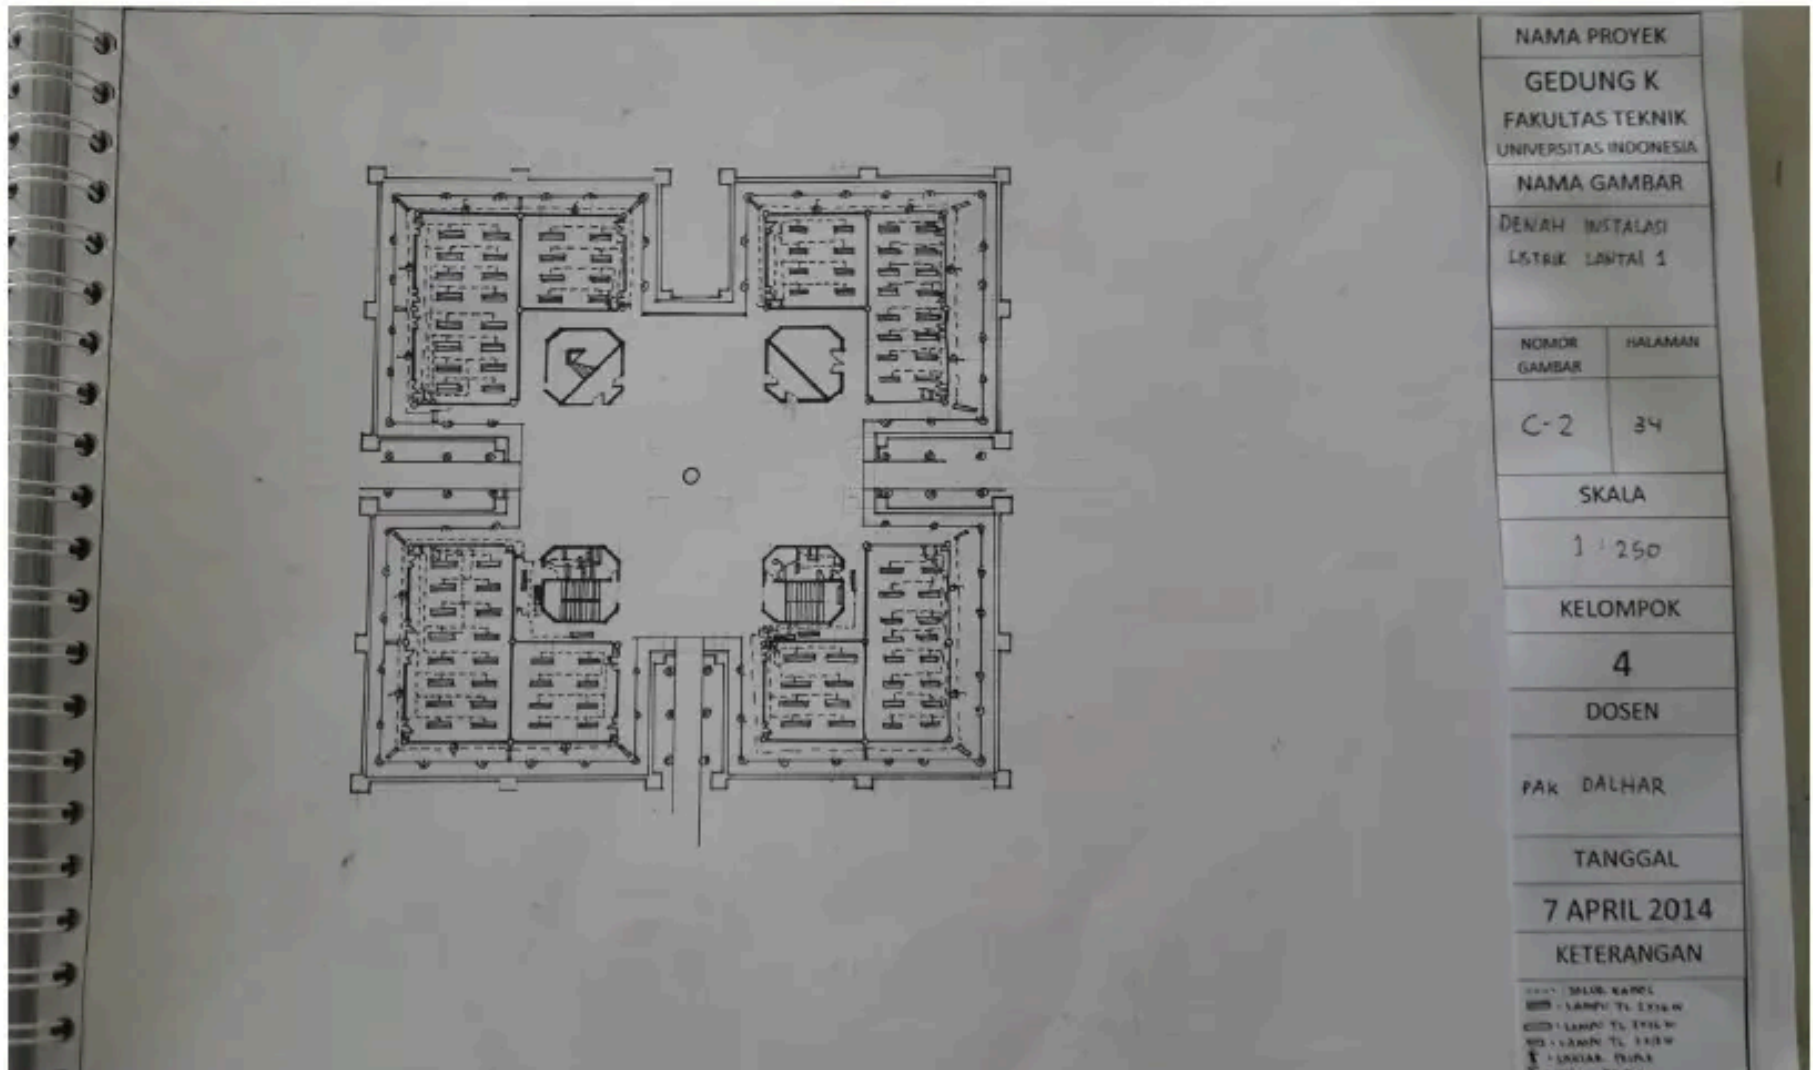

DENAH INSTALASI LISTRIK LANTAI 2

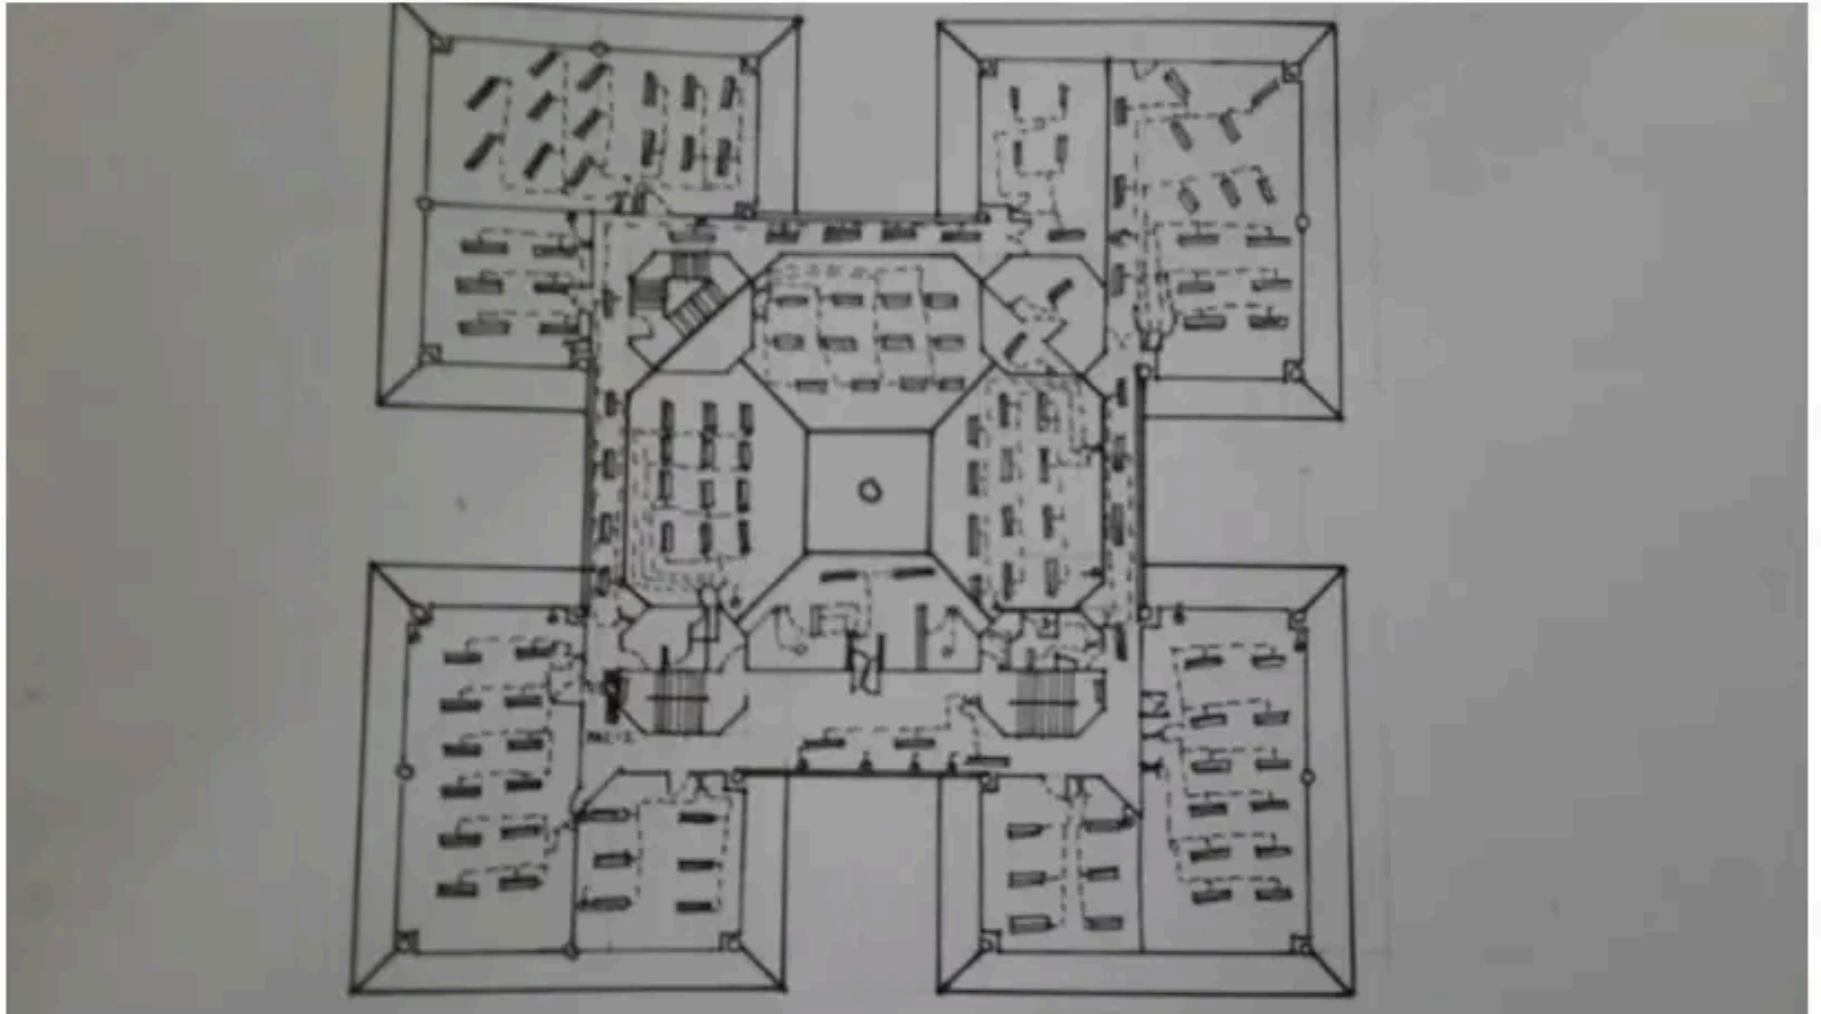


DENAH INSTALASI LISTRIK LANTAI 3

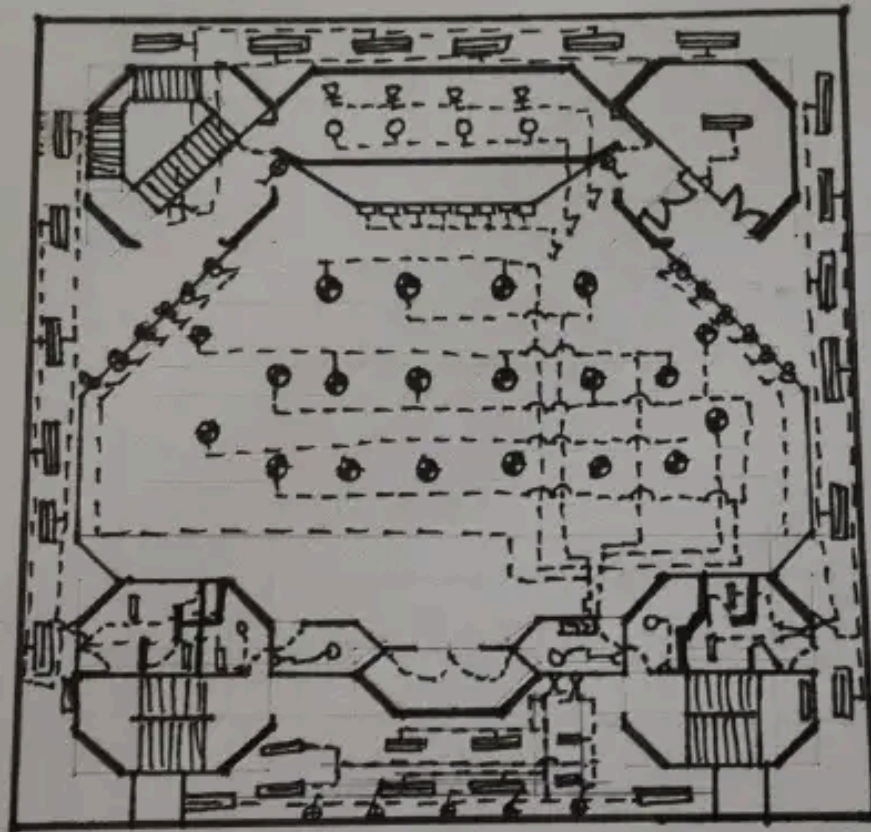

DETAIL INSTALASI ELEKTRIKAL (KHUSUS UNTUK FITTING DINDING)


PENYAMBUNGAN KABEL PADA STOPKONTAK

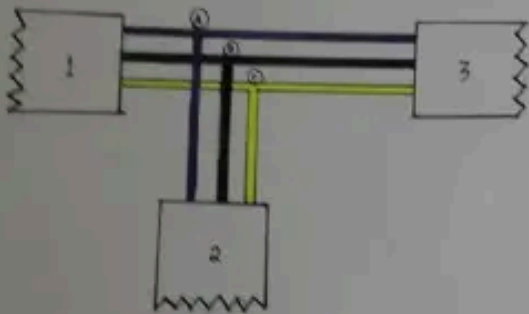

KETERANGAN GAMBAR :

1. KABEL 3X2,5 MM² TERHUBUNG DENGAN SUMBER LISTRIK.
2. KABEL 3X2,5 MM² TERHUBUNG DENGAN JALUR STOPKONTAK BARU.
3. KABEL 3X2,5 MM² TERHUBUNG DENGAN SALUR STOPKONTAK LAMA.
- A. SAMBUNGAN 3 KAWAT HITAM
- B. SAMBUNGAN 3 KAWAT BIRU
- C. SAMBUNGAN 3 KAWAT KUNING

PENYAMBUNGAN KABEL PADA SAKLAR T.

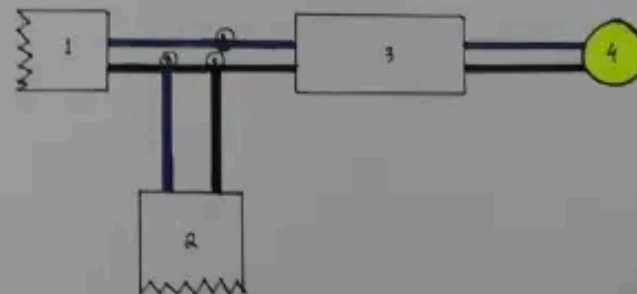

KETERANGAN GAMBAR :

1. KABEL 2X1,5 MM² TERHUBUNG DENGAN SUMBER LISTRIK / STOP KONTAK
2. KABEL 2X1,5 MM² TERHUBUNG DENGAN SAKLAR TUNGGA.
3. KABEL 2X1,5 MM² TERHUBUNG DENGAN LAMPU
4. UNIT LAMPU
- A. SAMBUNGAN 2 KAWAT BIRU BERGANDU ANTARA KABEL NO.1 DENGAN NO.2
- B. SAMBUNGAN KAWAT HITAM NO.1 DENGAN KAWAT BIRU NO.2
- C. SAMBUNGAN 2 KAWAT HITAM DARI KABEL NO.2 DENGAN NO.3

NAMA PROYEK

GEDUNG K

FAKULTAS TEKNIK

UNIVERSITAS INDONESIA

NAMA GAMBAR

DETAIL INSTALASI
ELEKTRIKAL (KHUSUS
FITTING DINDING)

NOMOR
GAMBAR

HALAMAN

SKALA

KELOMPOK

4

DOSEN

PAK DALHAR

TANGGAL

7 APRIL 2014

KETERANGAN

DIAGRAM DISTRIBUSI TELEPON DAN INTERNET


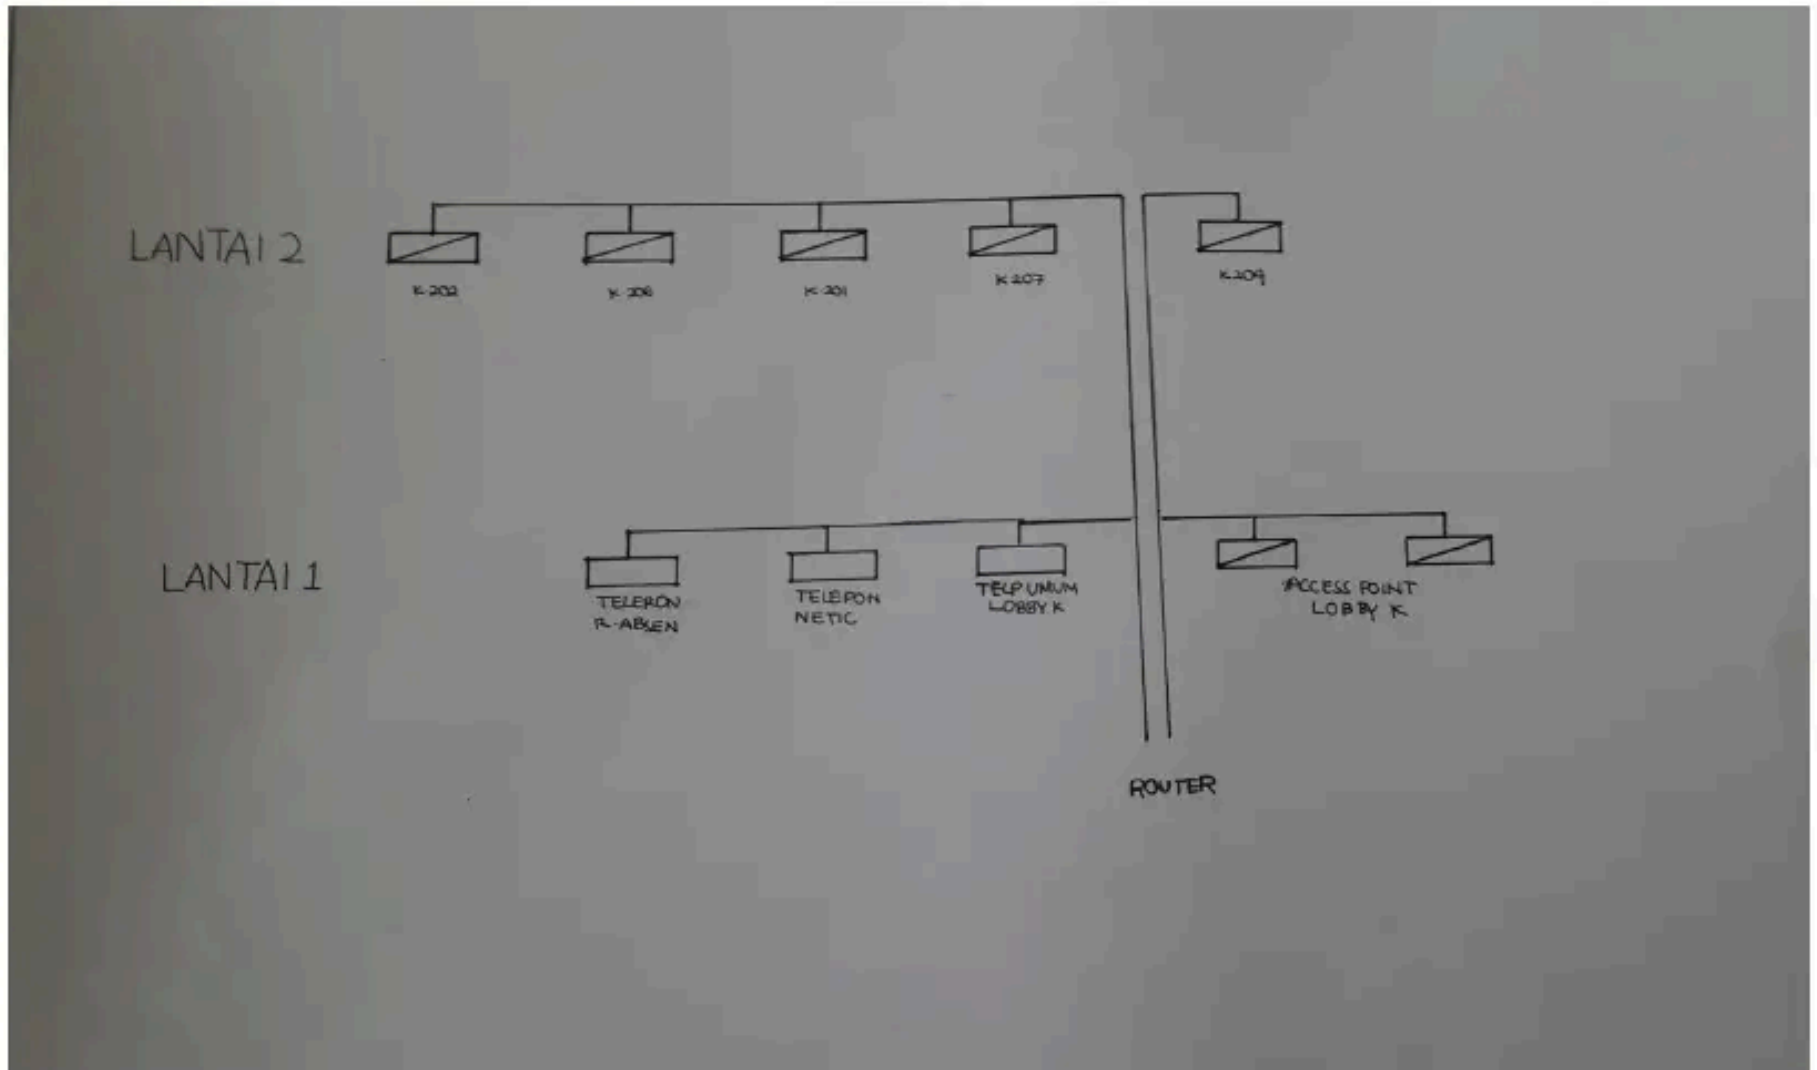


DIAGRAM DISTRIBUSI TATA SUARA

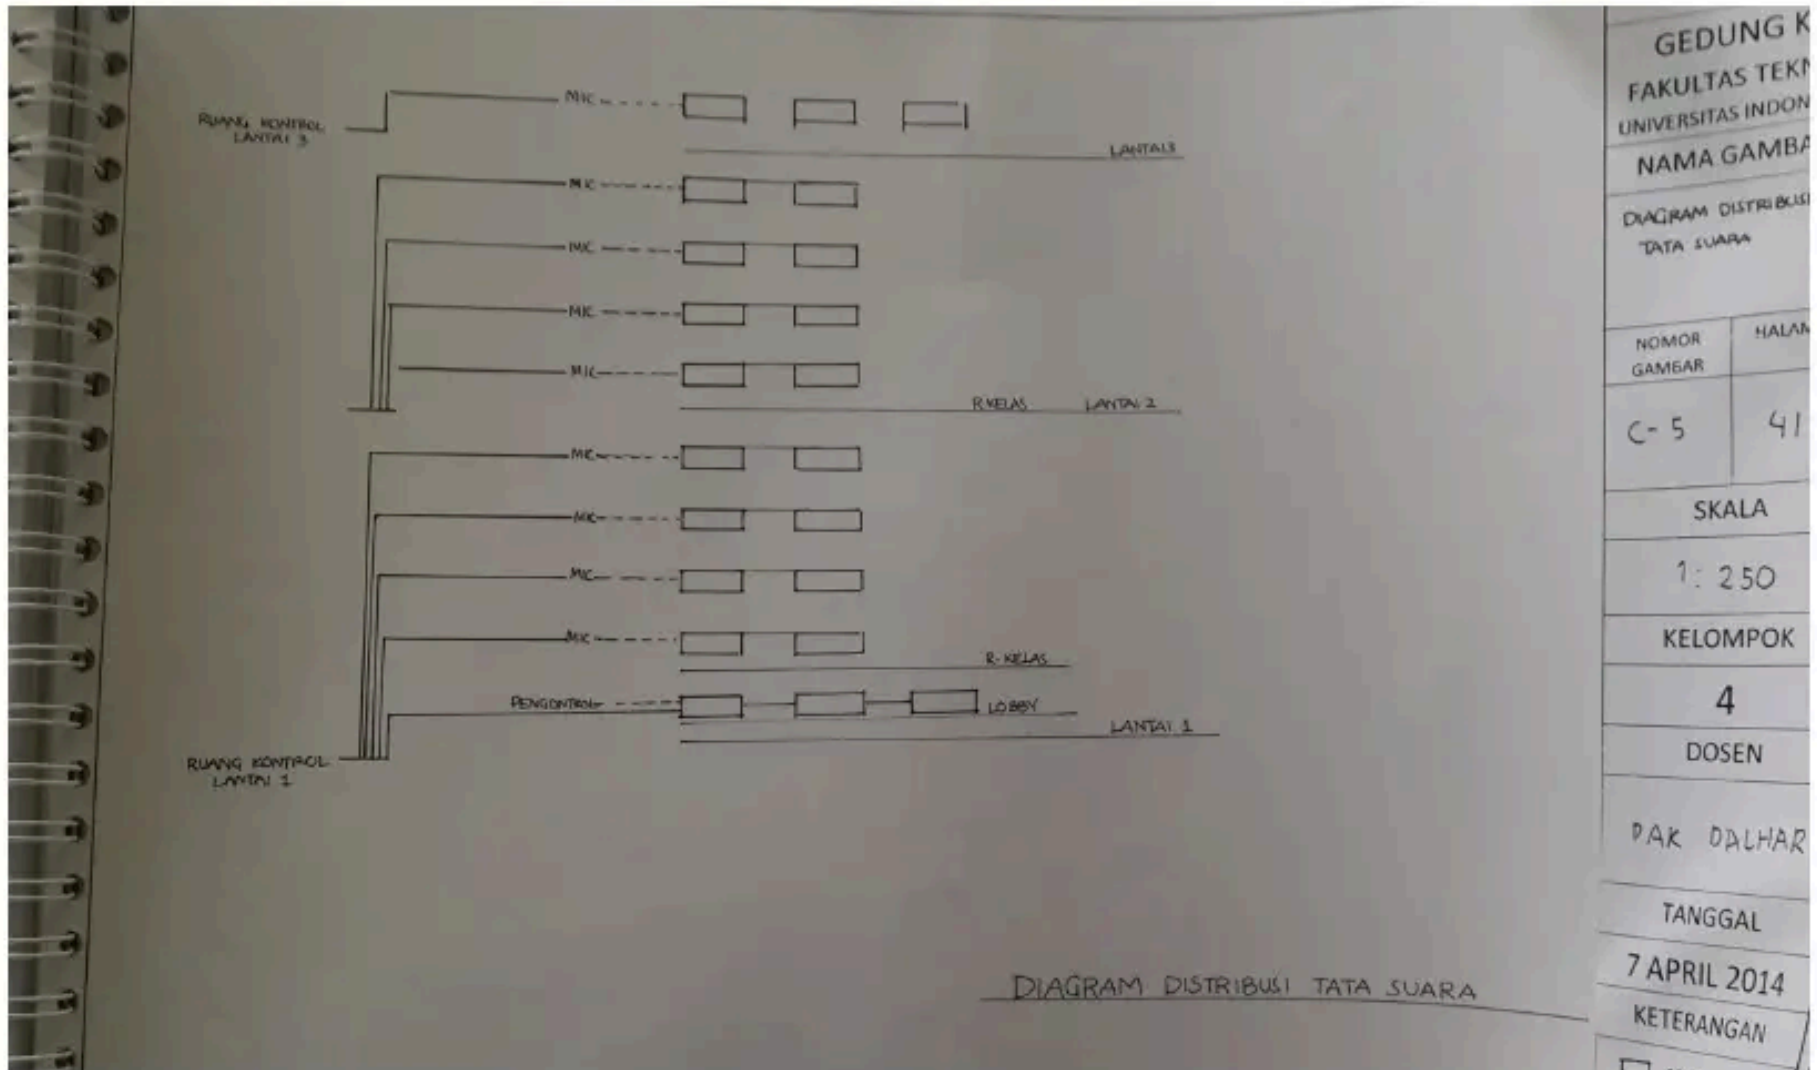

GEDUNG K
FAKULTAS TEKNI
UNIVERSITAS INDON
NAMA GAMBAR

DIAGRAM DISTRIBUSI
TATA SUARA

NOMOR GAMBAR	HALAMAN
C-5	41

SKALA
1: 250


KELOMPOK
4

DOSEN
PAK DALHAR


TANGGAL
7 APRIL 2014

KETERANGAN


DENAH INSTALASI TATA SUARA, TELEPON DAN INTERNET LT 1

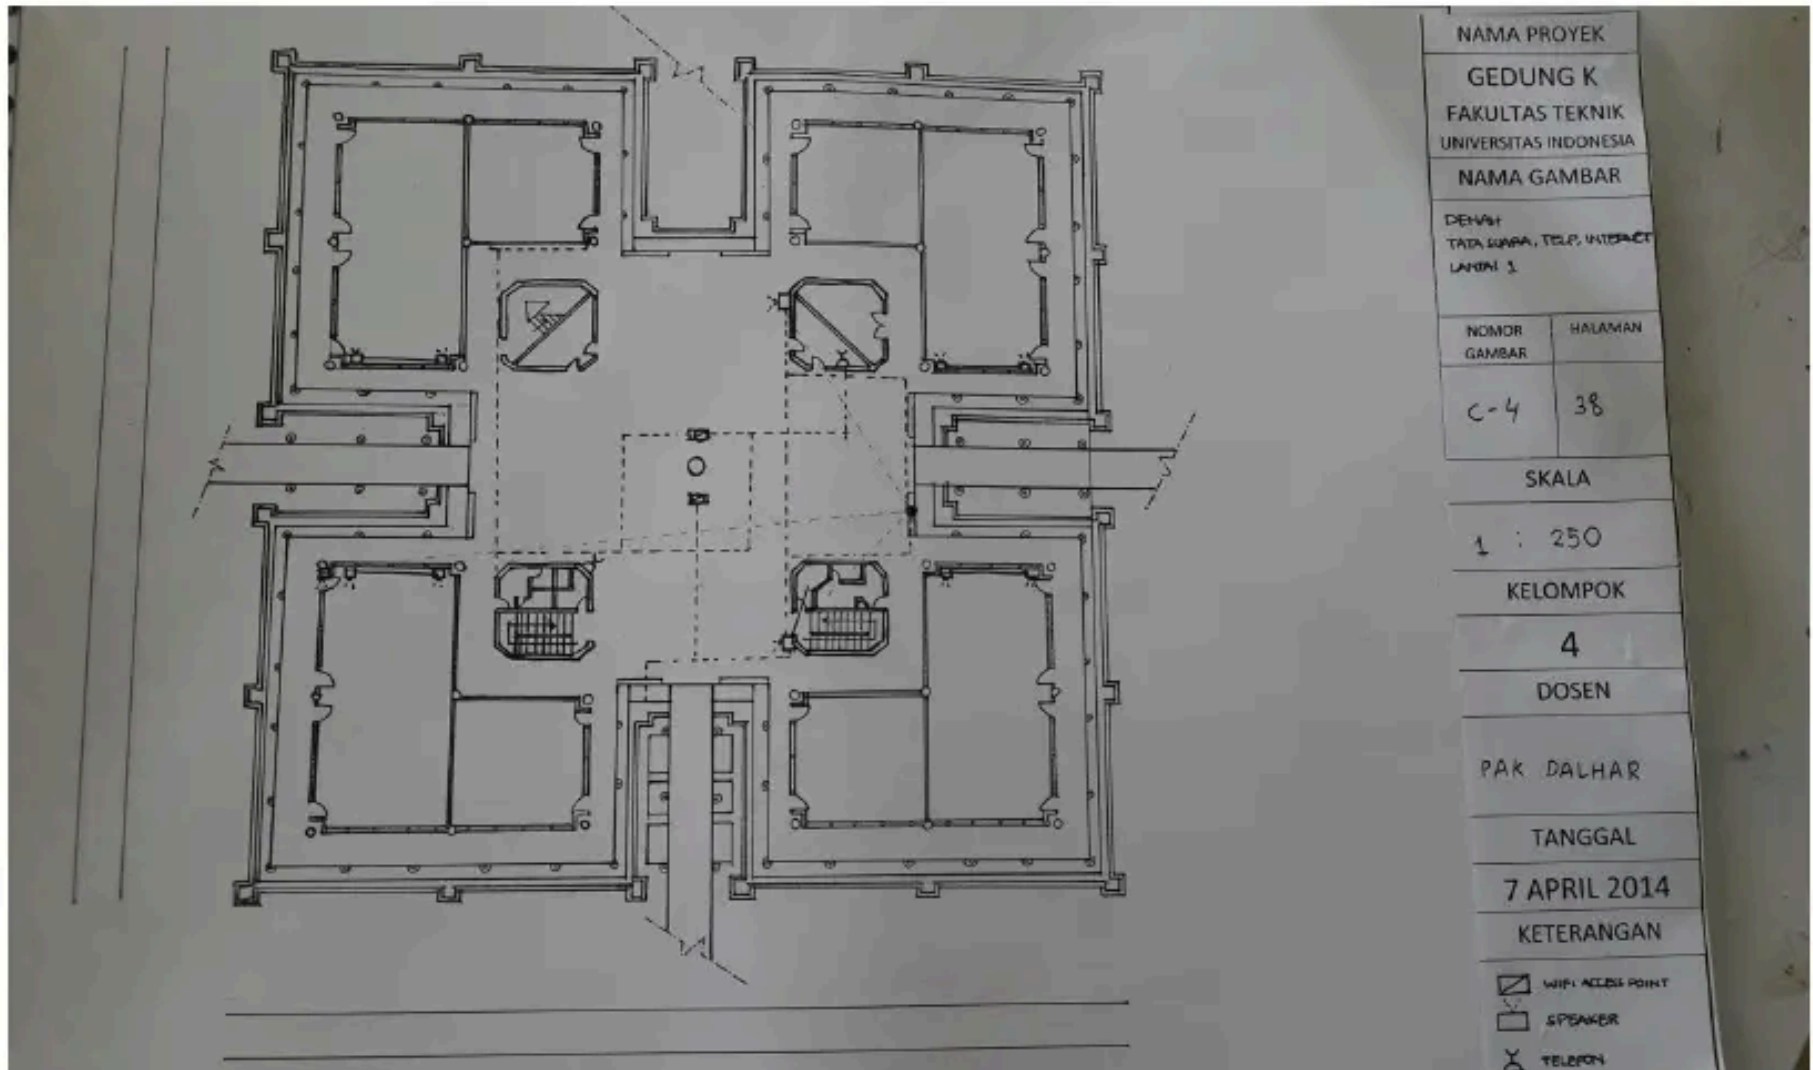

DENAH INSTALASI TATA SUARA, TELEPON DAN INTERNET LT 2

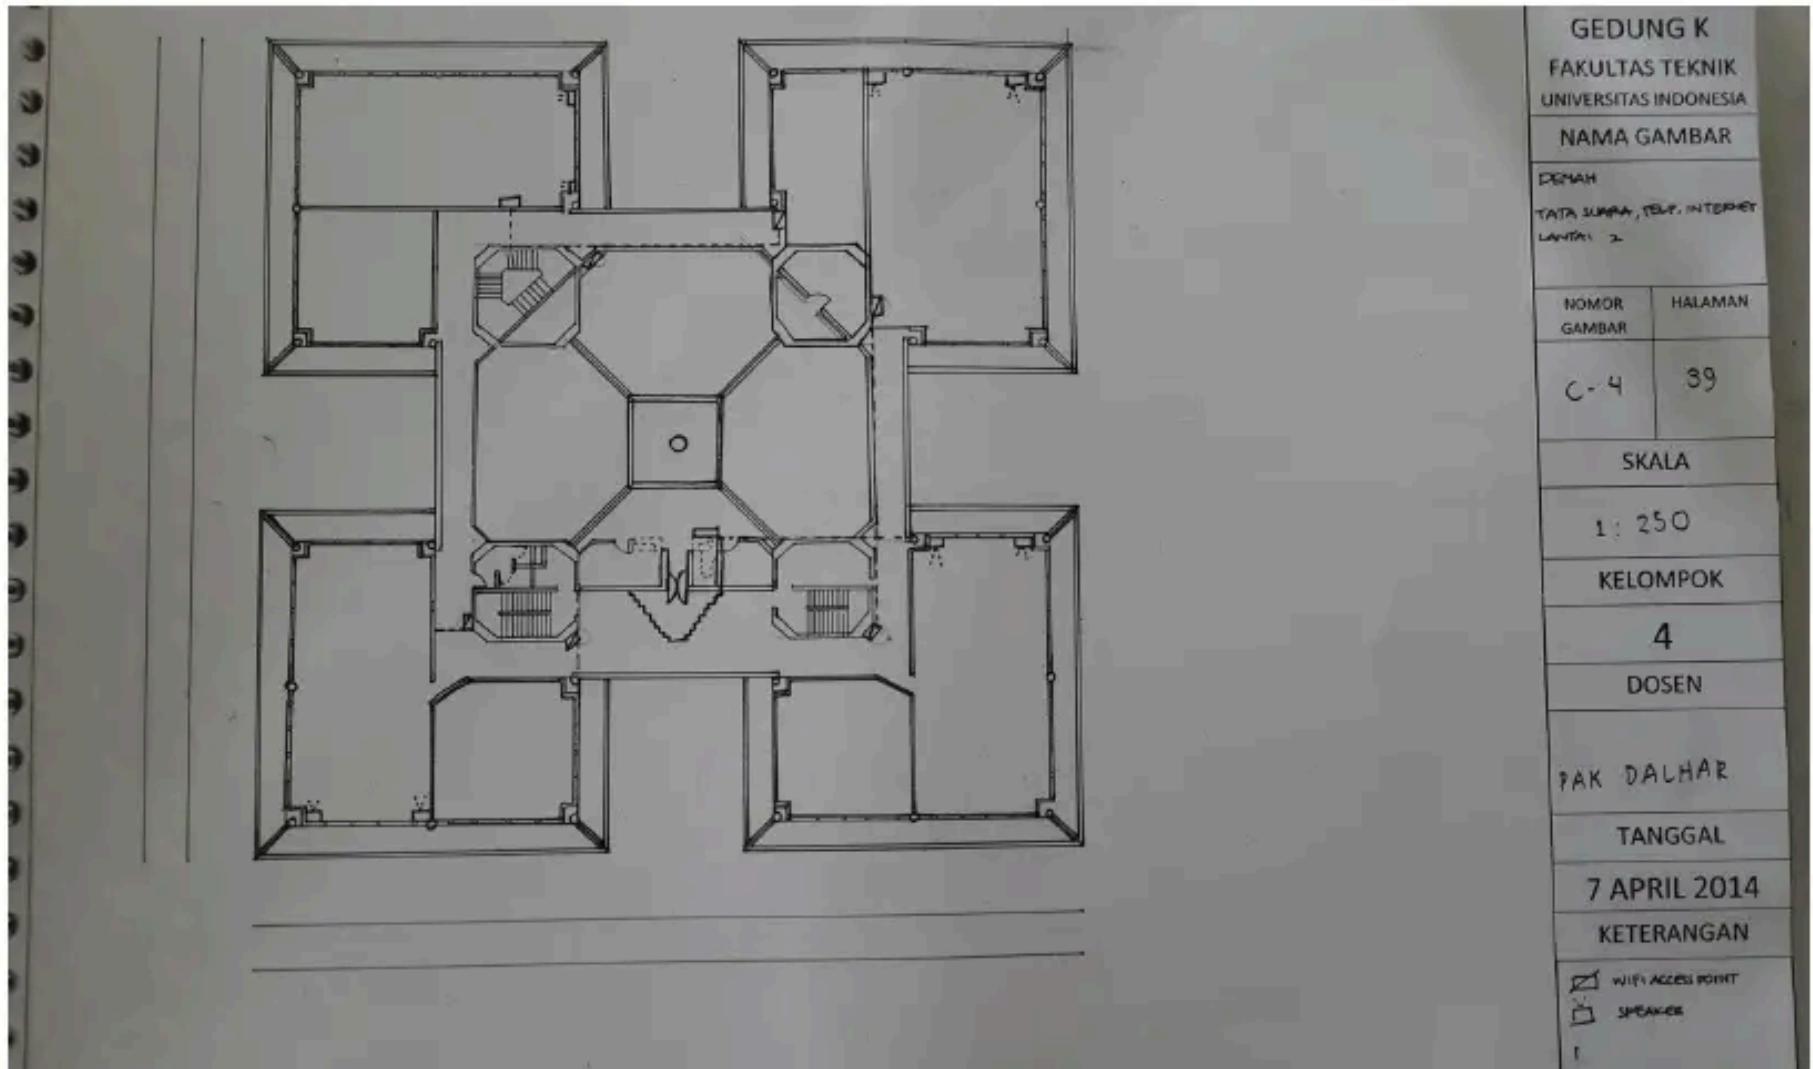

DENAH INSTALASI TATA SUARA, TELEPON DAN INTERNET LT 3

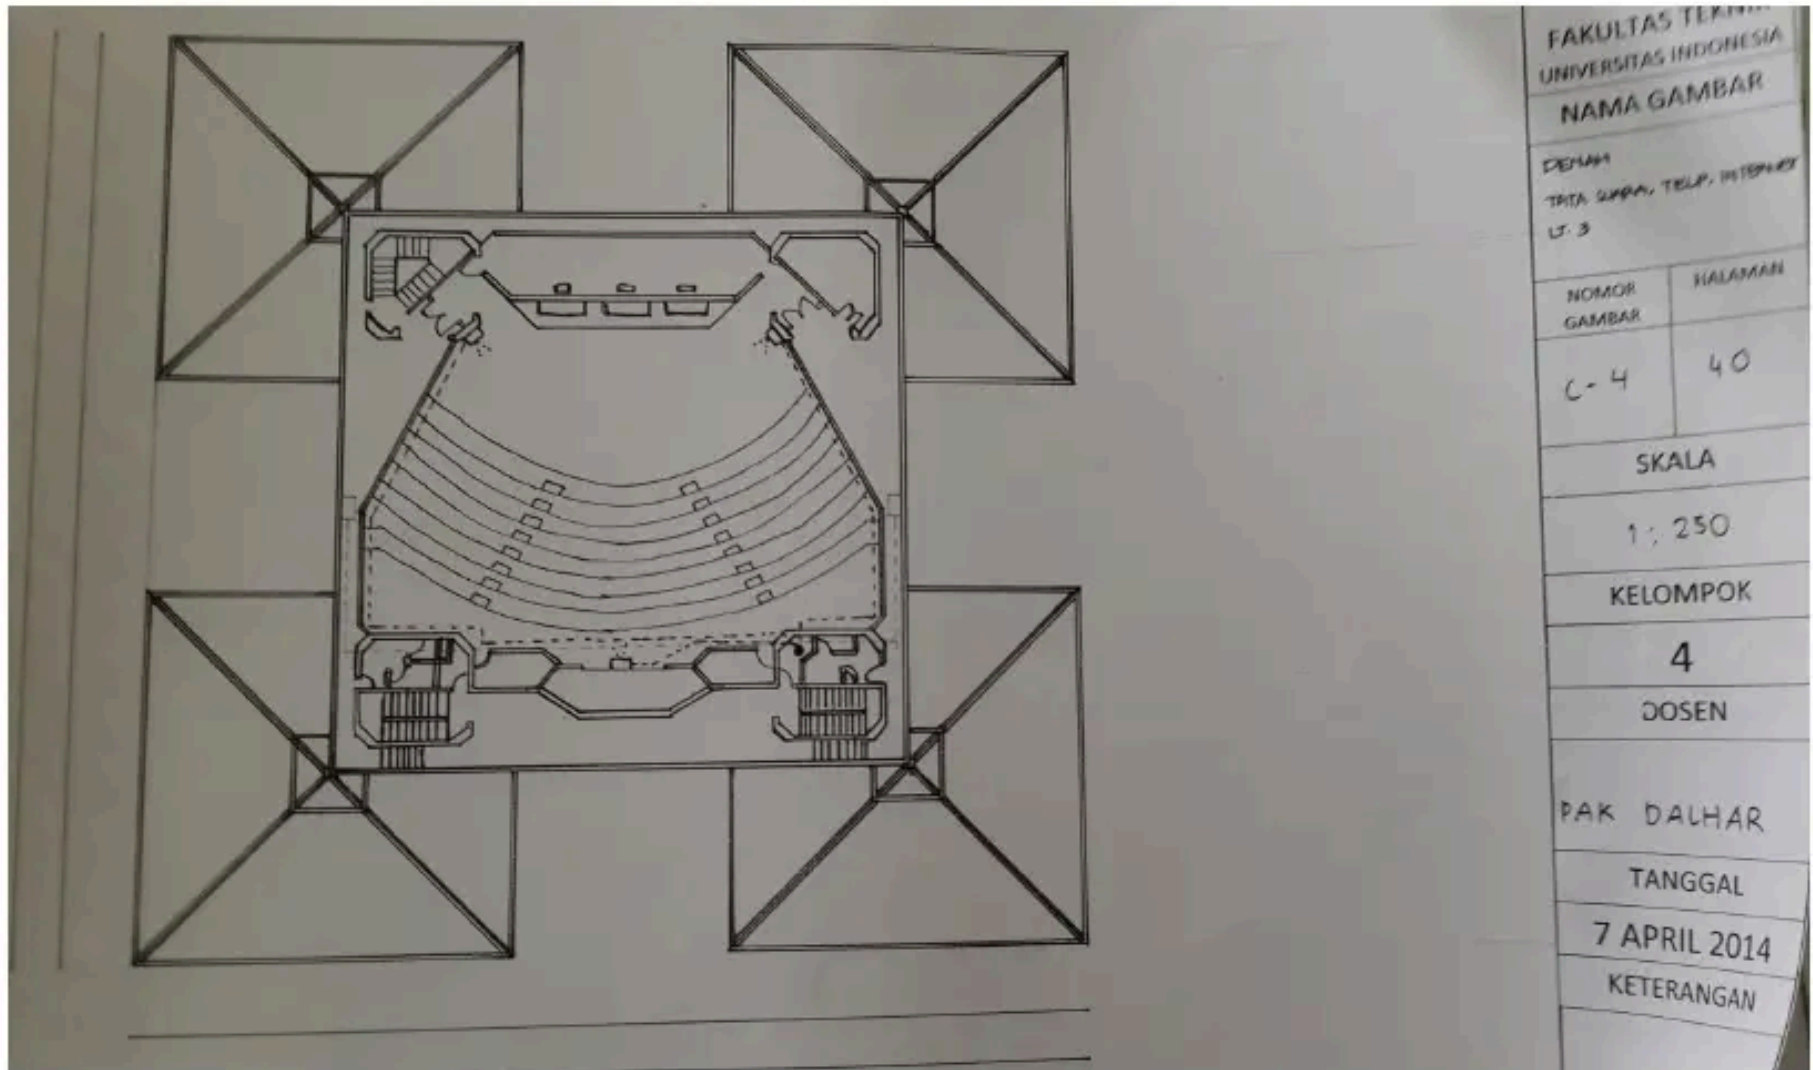

TERIMA KASIH
